


/ аэрофотосъемка / М1:2000

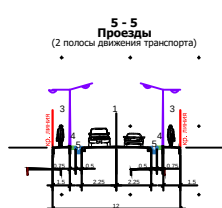


(размеры всех элементов даны в метрах):

- 1 - проезжая часть;
- 2 - краевые полосы /обочина/;
- 3 - тротуары;
- 4 - полосы озеленения; разделительные полосы;
- 5 - арочный лаоток

УСЛОВНЫЕ ОБОЗНАЧЕНИЯ

- | | |
|--|--|
| | Проектируемая граница с Аи-Терек |
| | Фактическая (сложившаяся) граница с Аи-Терек |
| | Проектируемые красные линии |
| | Автодорога республиканского значения |
| | Основные пешеходные связи |
| | Главные поселковые улицы |
| | Улицы местного значения |
| | Общекурортный бульвар |
| | АЗС / авто заправочная станция / |
| | Автостоянка |
| | Озера, реки, магистральные каналы, водоемы |

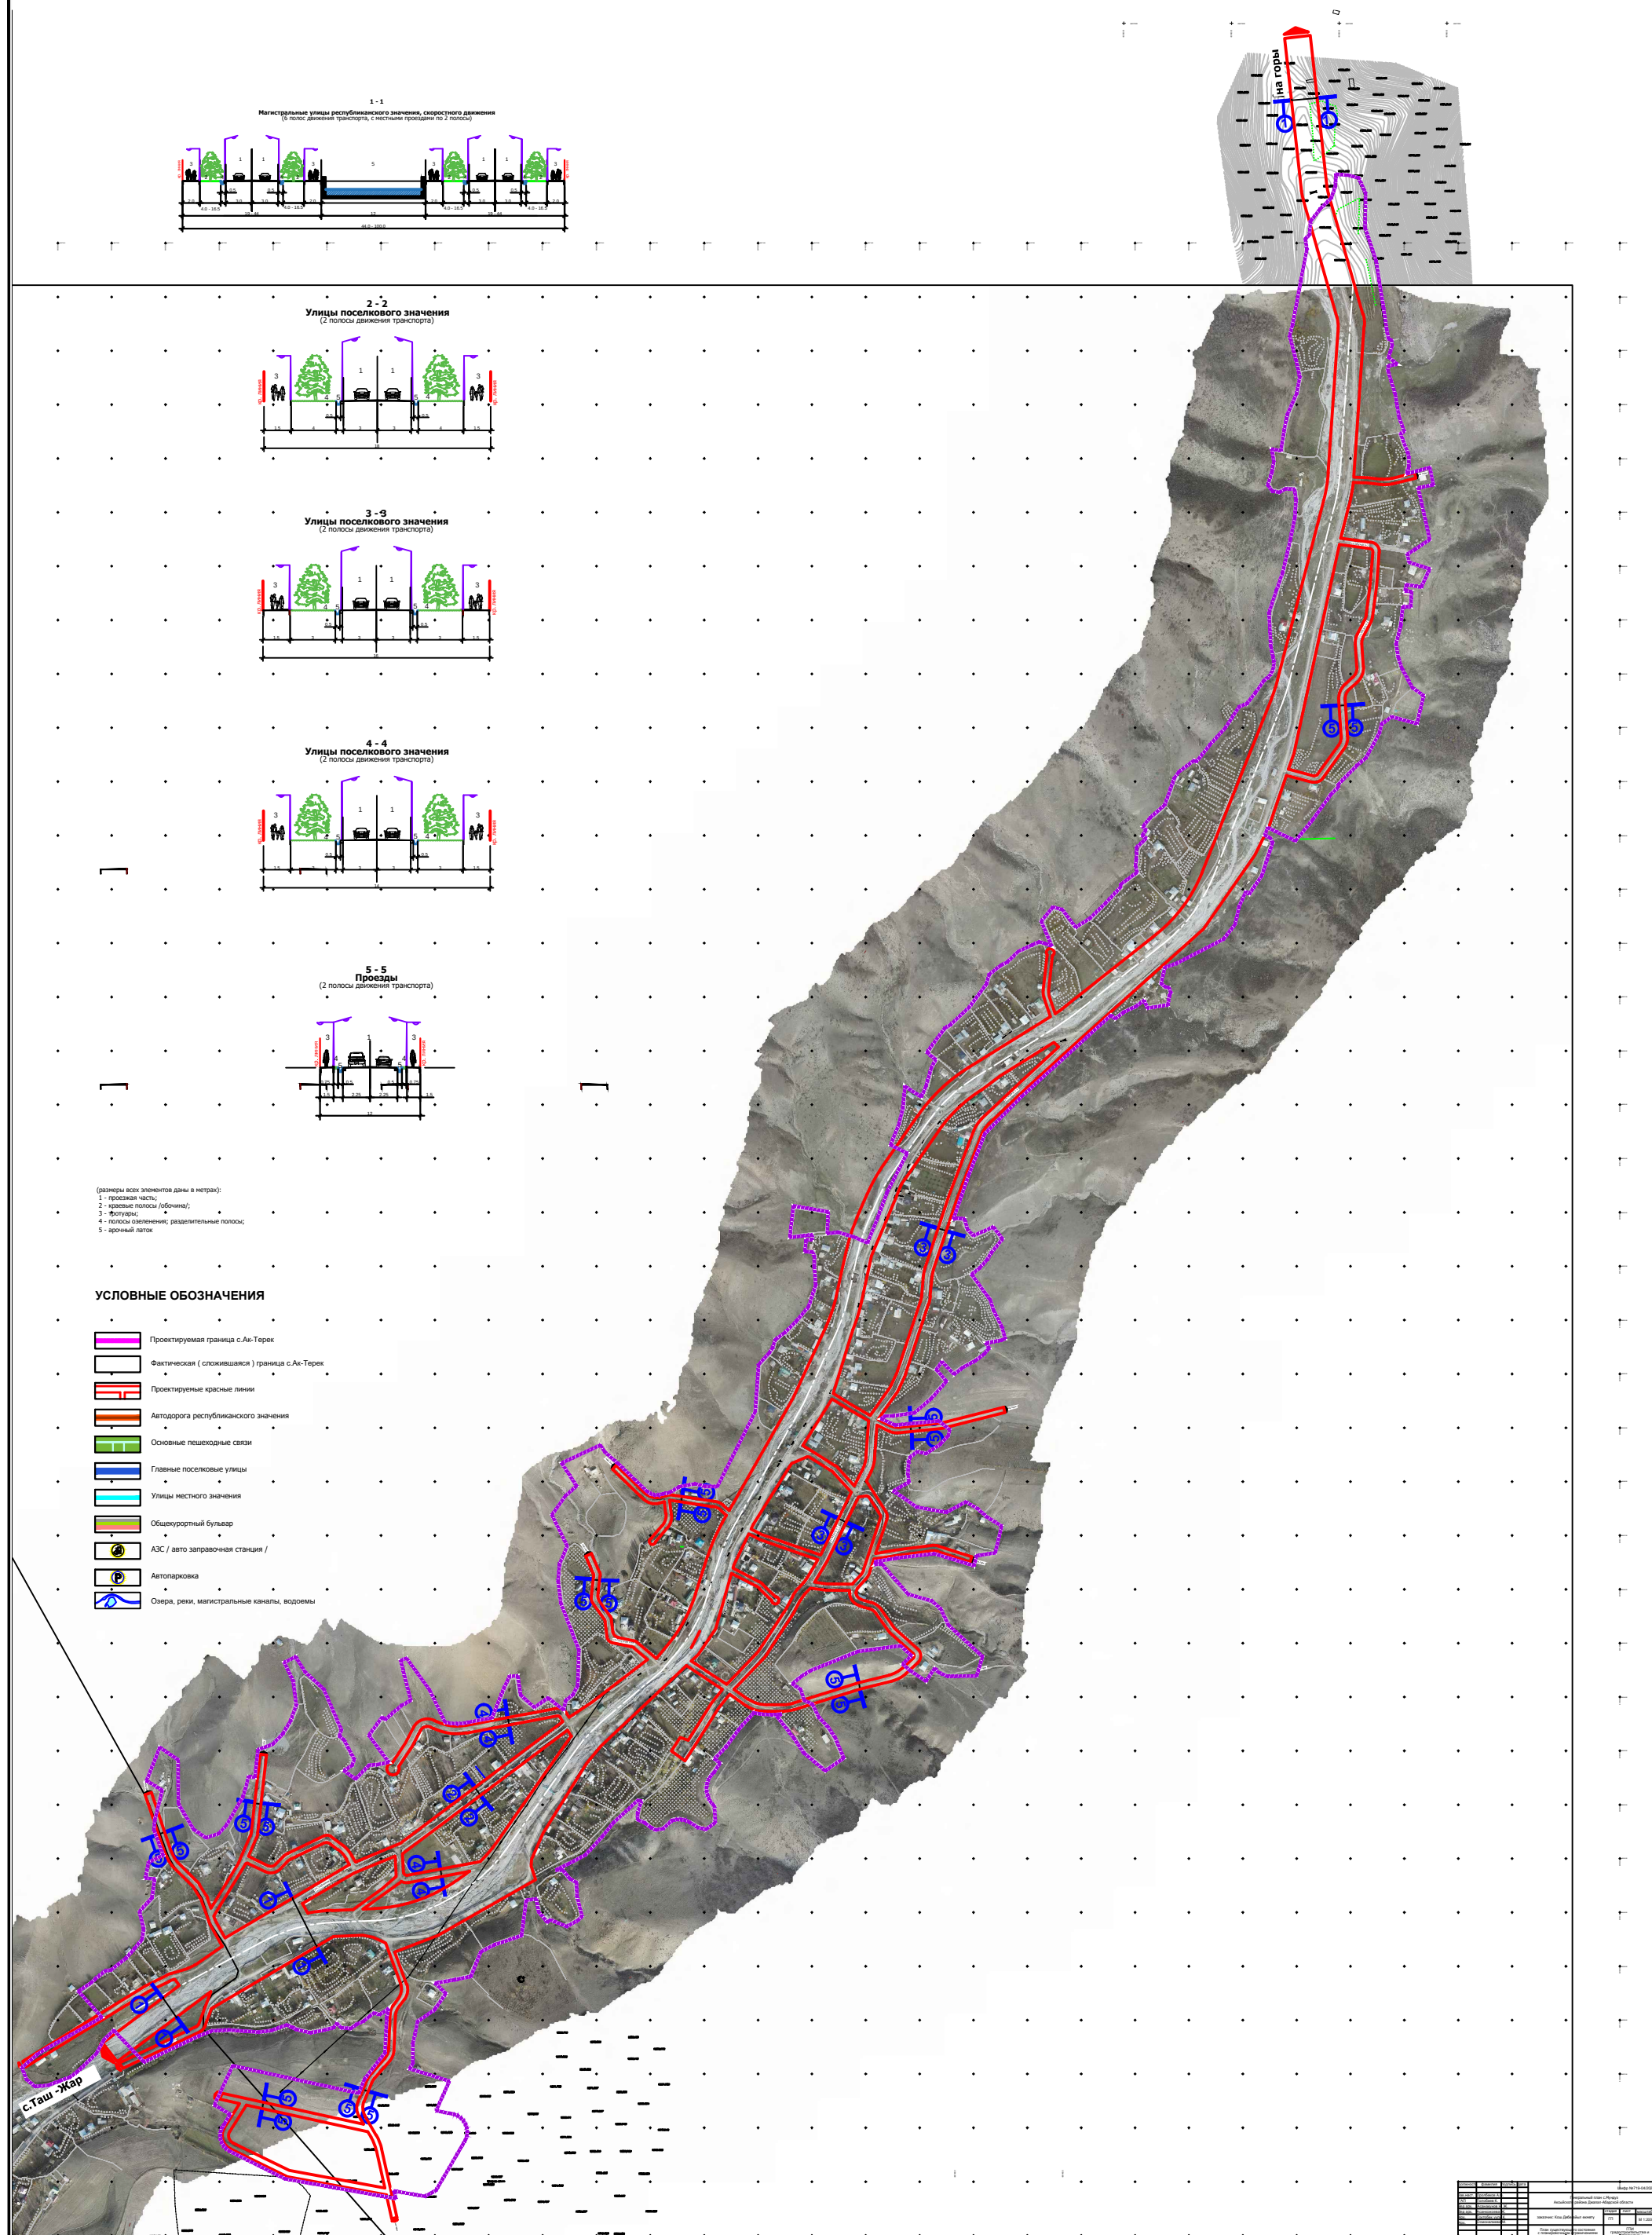[illegible]