


ГЕНЕРАЛЬНЫЙ ПЛАН с.ЖАҢҒАК АКСЫЙСКОГО РАЙОНА ЖАЛАЛ-АБАДСКОЙ ОБЛАСТИ

СХЕМА УЛИЧНО - ДОРОЖНОЙ СЕТИ И ВНЕШНЕГО ТРАНСПОРТА

/ аэрофотосъемка / М 1:2000

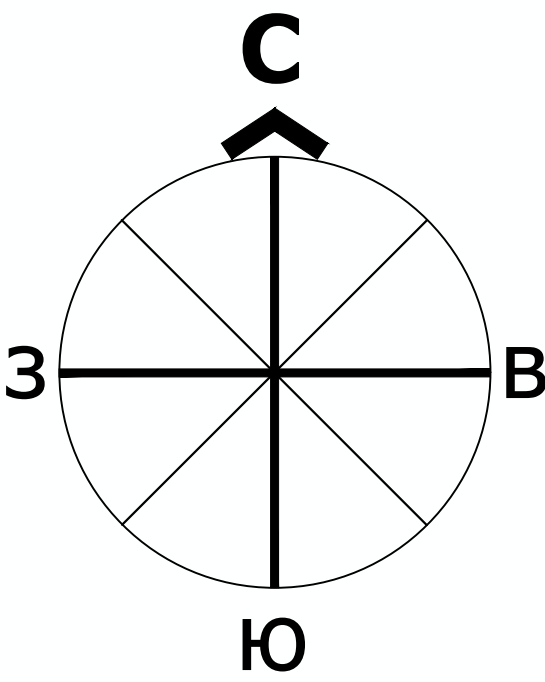


УСЛОВНЫЕ ОБОЗНАЧЕНИЯ


- Фактическая (сложившаяся) граница с. Жангак
- Проектируемая граница с. Жангак
- Проектируемые красные линии
- Мосты и переправы
- Одноуровневые транспортные узлы

с.ЖАҢҒАК


5 - 5
Улицы местного значения
(2 полосы движения транспорта)

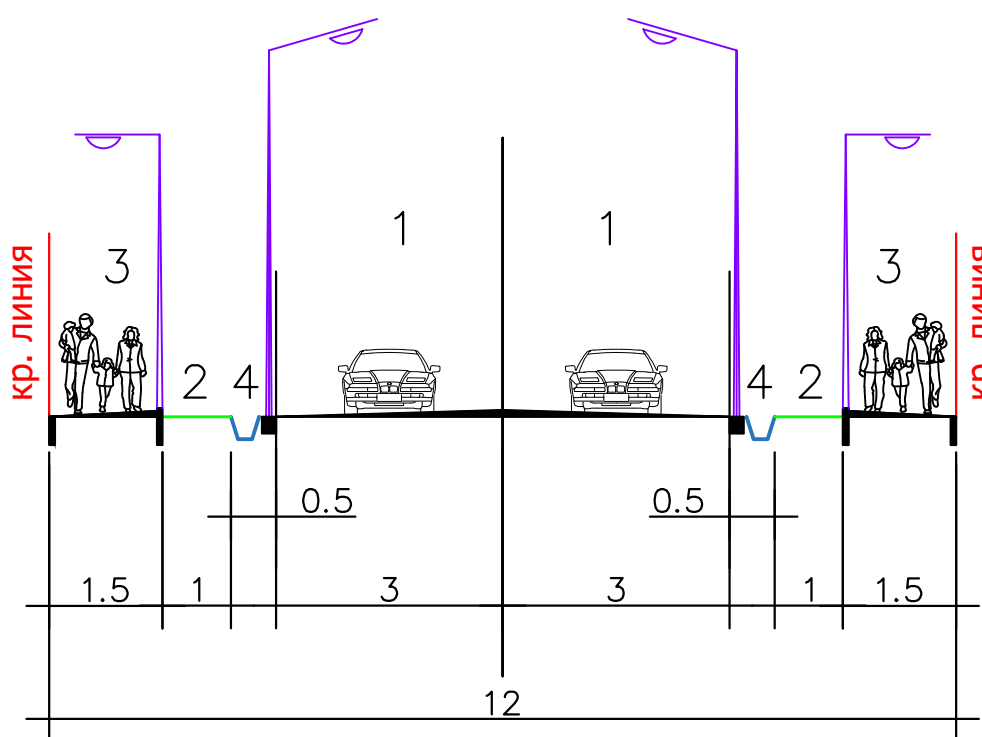


4 - 4
Улицы местного значения
(2 полосы движения транспорта)

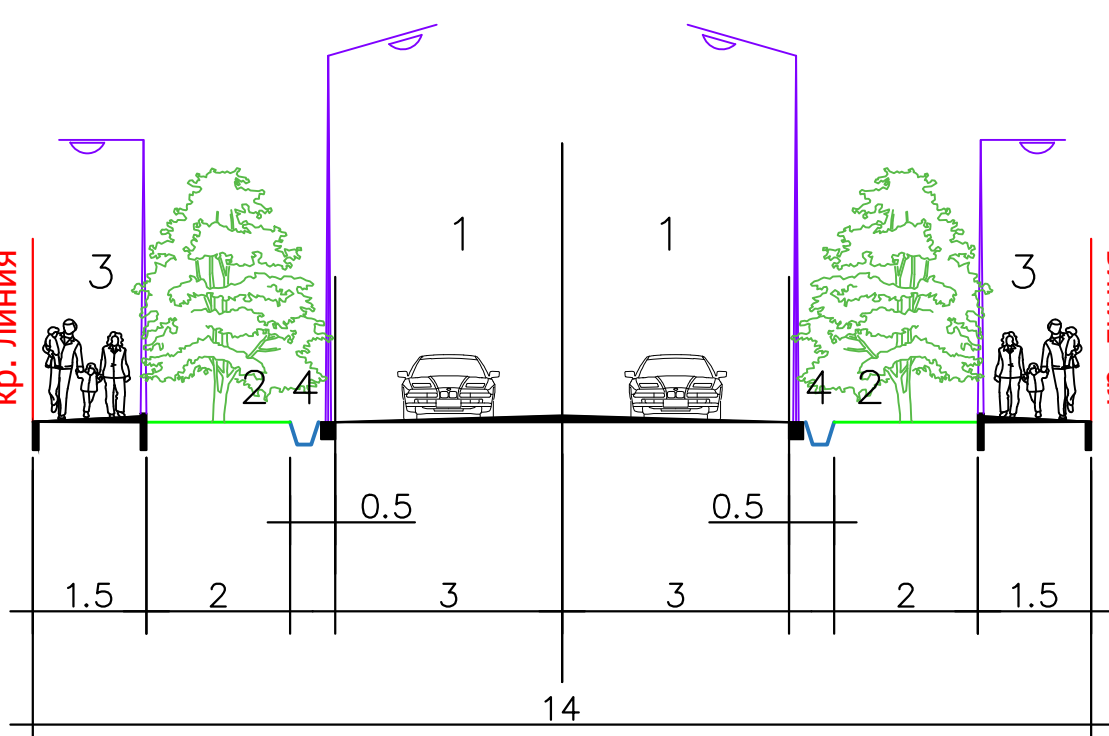


3 - 3
Улицы местного значения
(2 полосы движения транспорта)

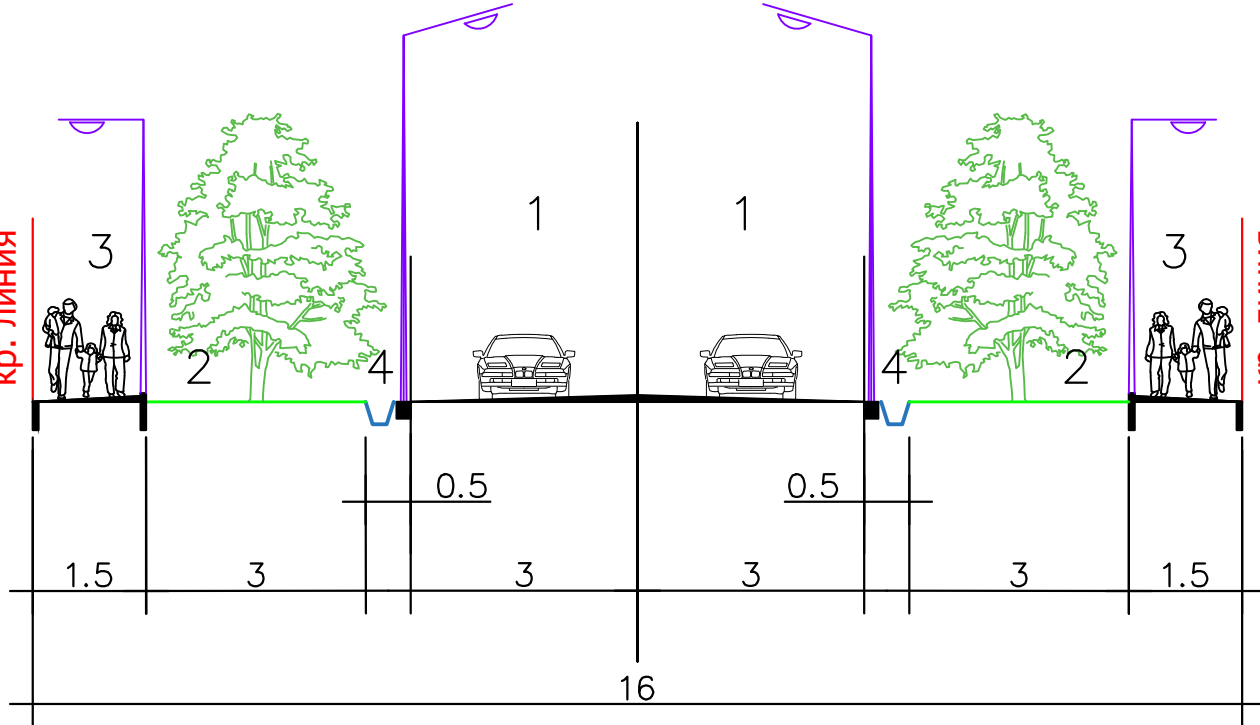

2 - 2
Улицы общепоселкового значения
регулируемого движения
(2 полосы движения транспорта)

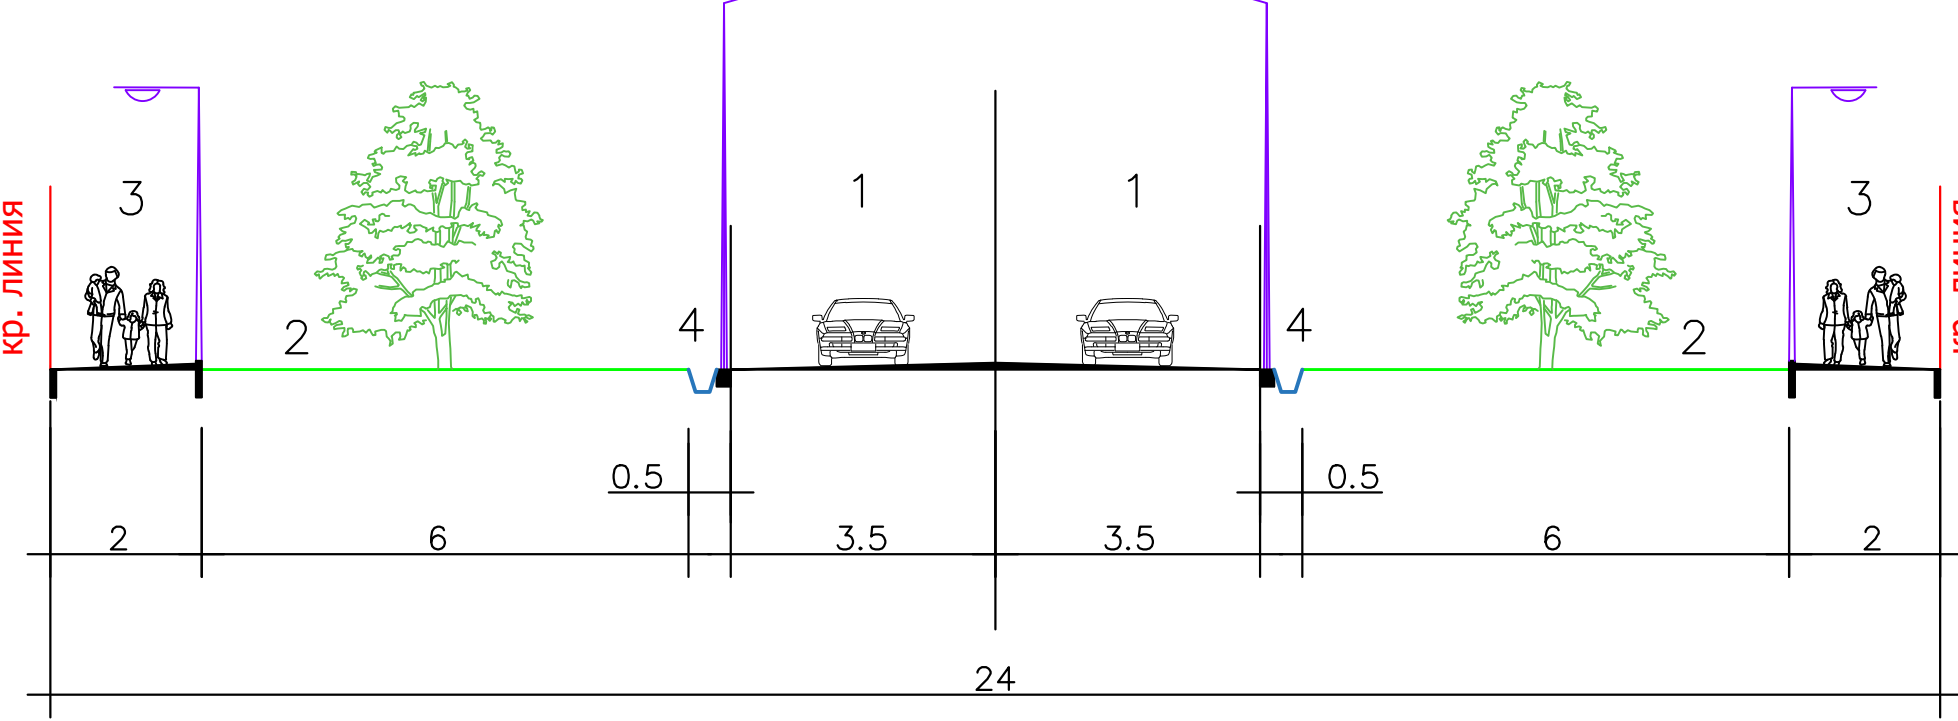

1 - 1
Улицы общепоселкового значения
регулируемого движения
(4 полосы движения транспорта)

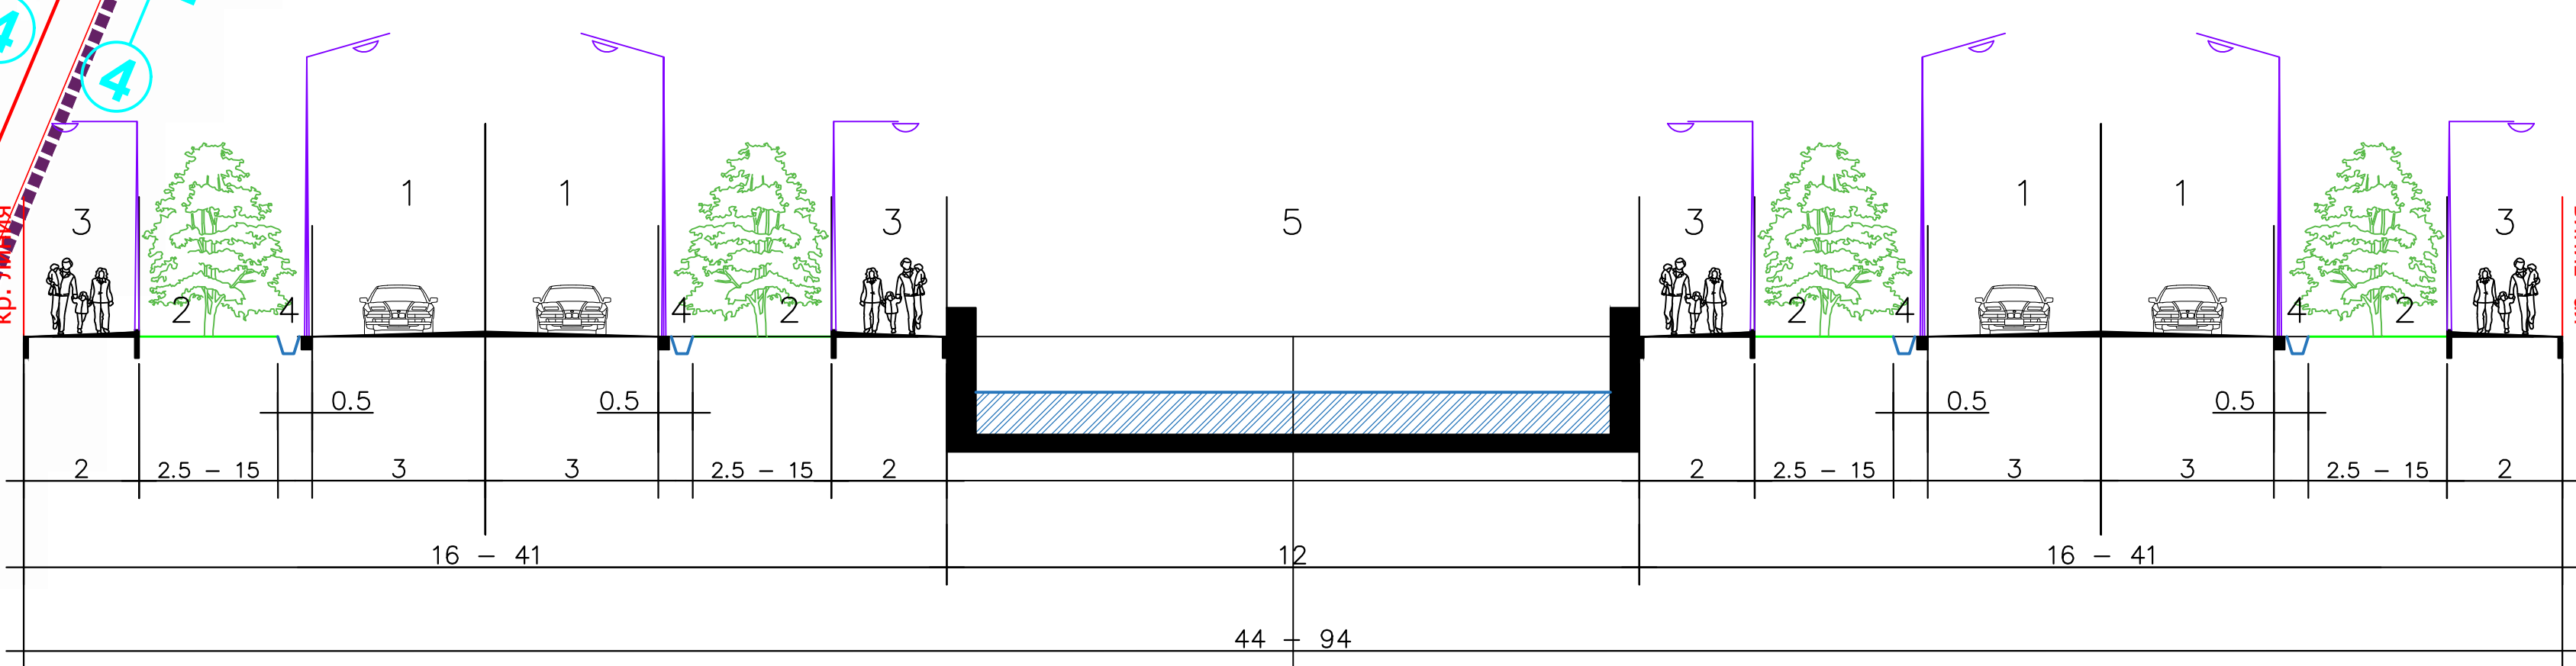

(размеры всех элементов даны в метрах):

- 1 - проезжая часть;
- 2 - полосы озеленения; разделительные полосы;
- 3 - тротуары;
- 4 - арочный латок
- 5 - селеотводной канал

должность	фамилия	подпись	Шифр №300-04/2023		
зам. намест.	Ордабаева А.Д.		Генеральный план с.Жангак		
ГАП	Толгобаев Х.		Аксыйского района Жалал-Абадской области		
АР	Тоттобаев у.К.		заказчик: Кош-Дорбе айыл окуту		
			стадия	лист	масштаб
			ГП	1	М 1:2000
				ГП	ГП
					градостроительства и
					архитектуры