
 


/ схема территориального развития / М1:2000

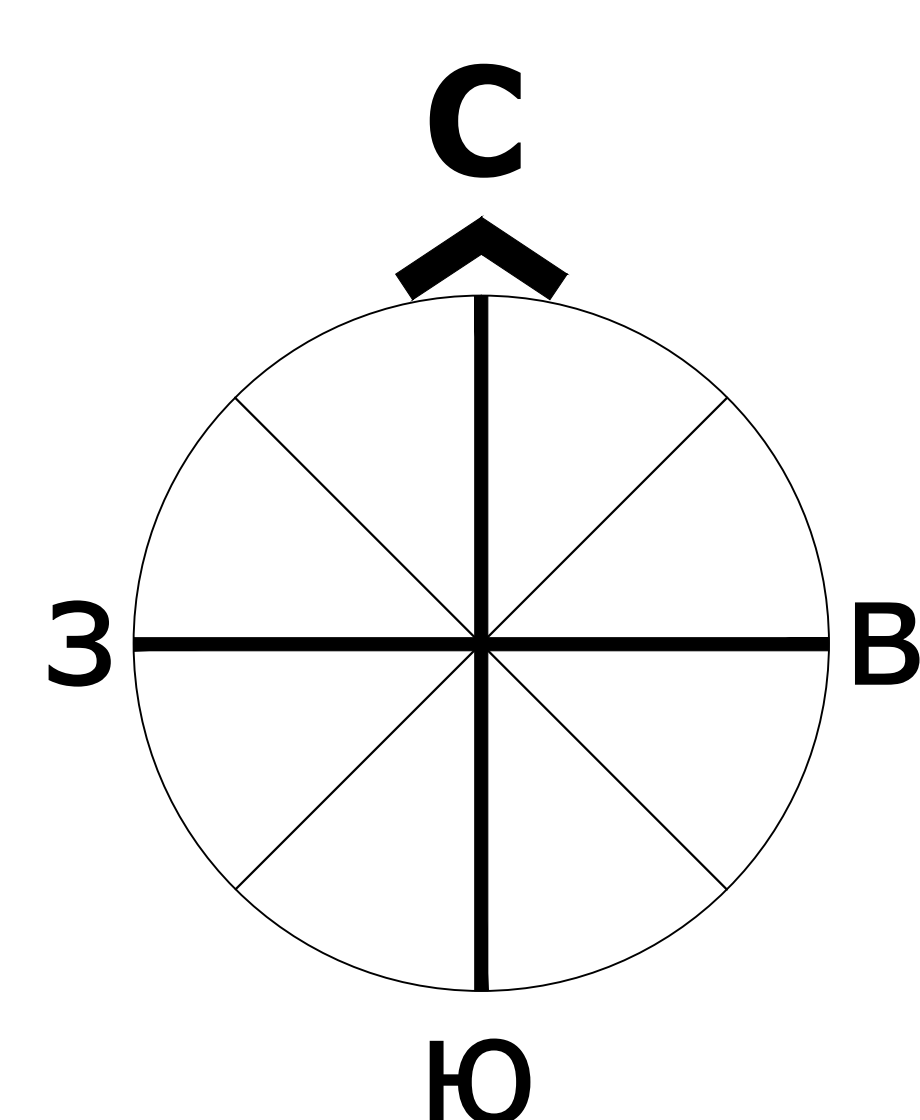

ОСНОВНЫЕ ТЕХНИКО-ЭКОНОМИЧЕСКИЕ ПОКАЗАТЕЛИ
ГЕНЕРАЛЬНОГО ПЛАНА села Удуг

№ п/п	Наименование	Единица измерения	Исходный год-2013	Расчетный период 2016г.
1	2	3	4	5
1	Население: численность населения, удельный вес населения в трудоспособном возрасте трудовые ресурсы	тыс.чел. % %	1562	2265
2	Территория в границах села всего в том числе: 1. Селитбеговая территория из них: - земля: - участки зданий, учреждений обслуживания и спортивных сооружений - зеленые насаждения общего пользования - магистрал Протяженность магистралей	га га га га га га кч	124,5 124,5 2,8 1,2 23,8	142,4 118,2 2,8 1,2 37,8
2	Внеселитбеговая территория Общий жилой фонд	га дом	23,9	13,3

договорность	фамилия	подпись	№716-04/2024 от 09.09.2024г.		
зам.мэст.	Орловская А.О.		Генеральный план с.Улук Адылского района Жапан-Абдасово к.б. заказчик: Коср-Добо айыл оомуту Схема территориального развития		
г.а.п.	Топобаев К.				
вед. з.р.	Асанжурова Н.Ж.				
вед. з.р.	Асанжурова Ж.М.				
вед. з.р.	Адырмыны А.				
вед. з.р.	Адырмыны А.		этадия	лист	масштаб
вед. з.р.	Туктобе уулу К.				
з.р.	Осмоналиева М.				
			ГП		М 1:2000
			ГП		
			градостроительства и архитектуры		