



M1:2000

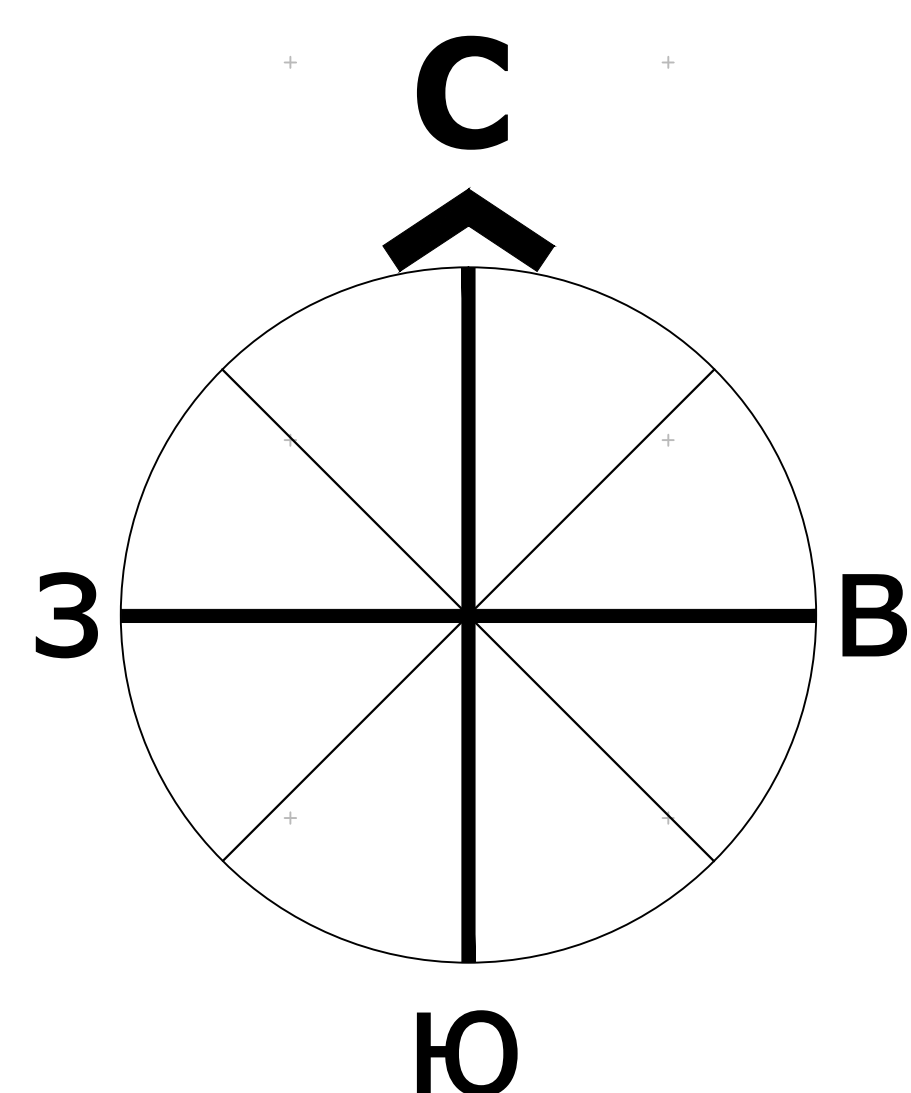


	Фактическая (сложившаяся) граница
	Проектируемая граница
	Проектируемые красные линии
	Реки, магистральные каналы, водоемы
	Главные поселковые улицы
	Улицы и дороги местного значения
	Проезды
	Мосты и переправы


1. Школа им. Ж.Султанова №98 на 225 учащихся мест
2. Детский сад С.Касымбекова на 50 учащихся мест
3. Стадион
4. Проектируемый ФАП
5. Проектируемый детский сад
6. Проектируемая спортивная школа

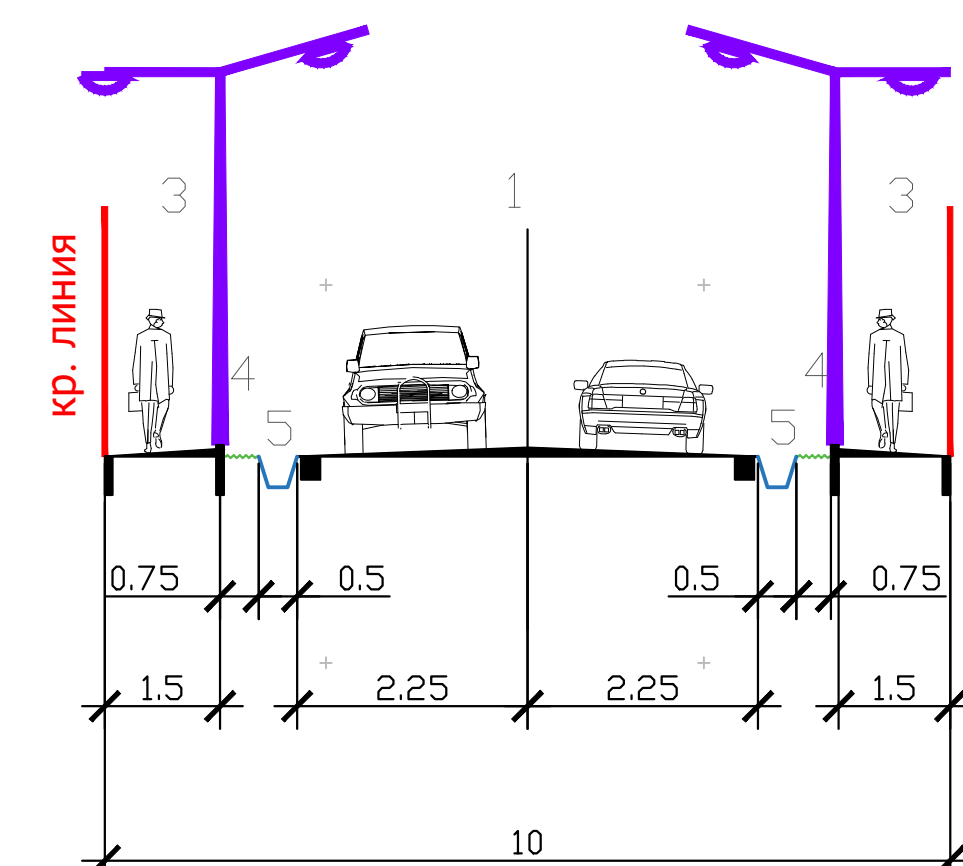


3 - 3
Улицы местного значения
(2 полосы движения транспорта)

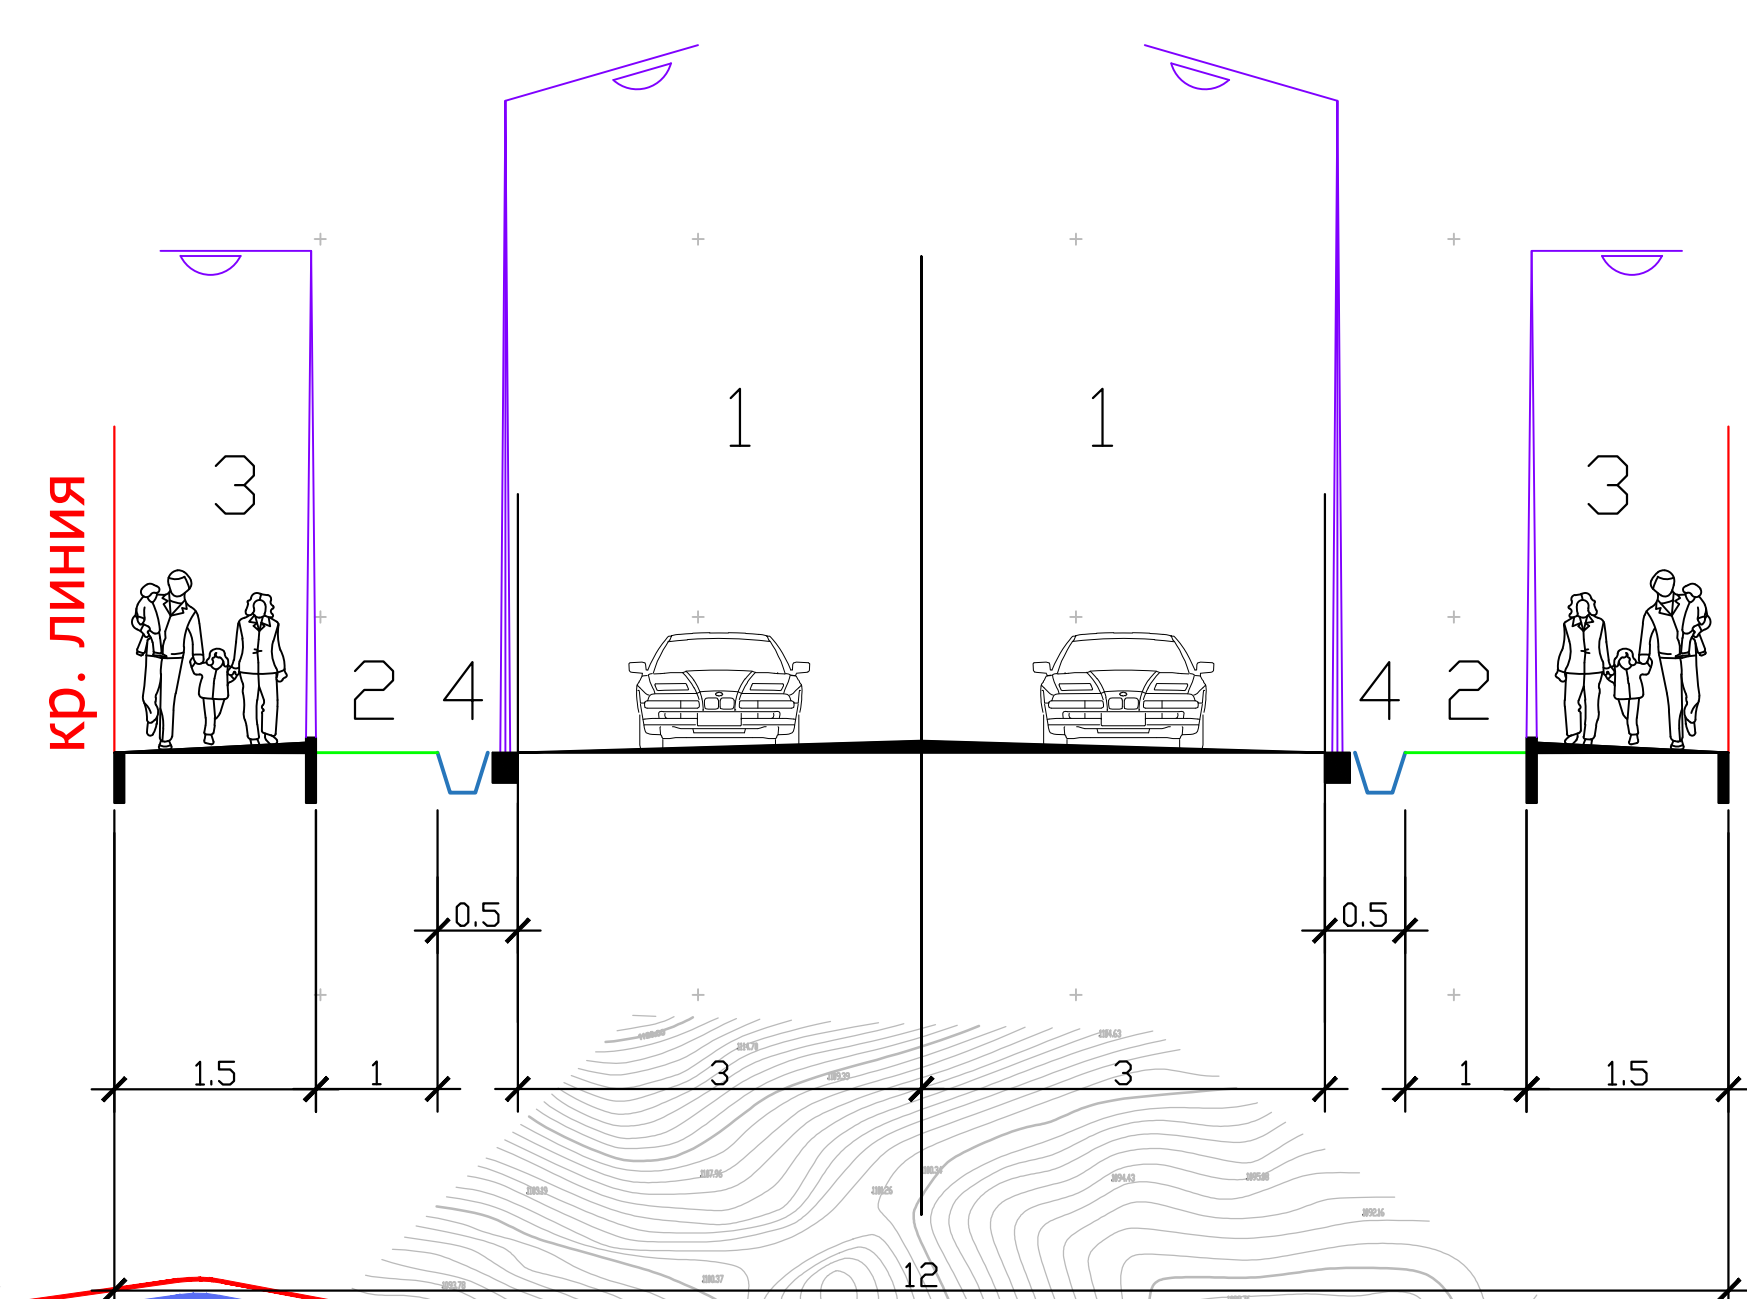


2 - 2
Улицы местного значения
(2 полосы движения транспорта)

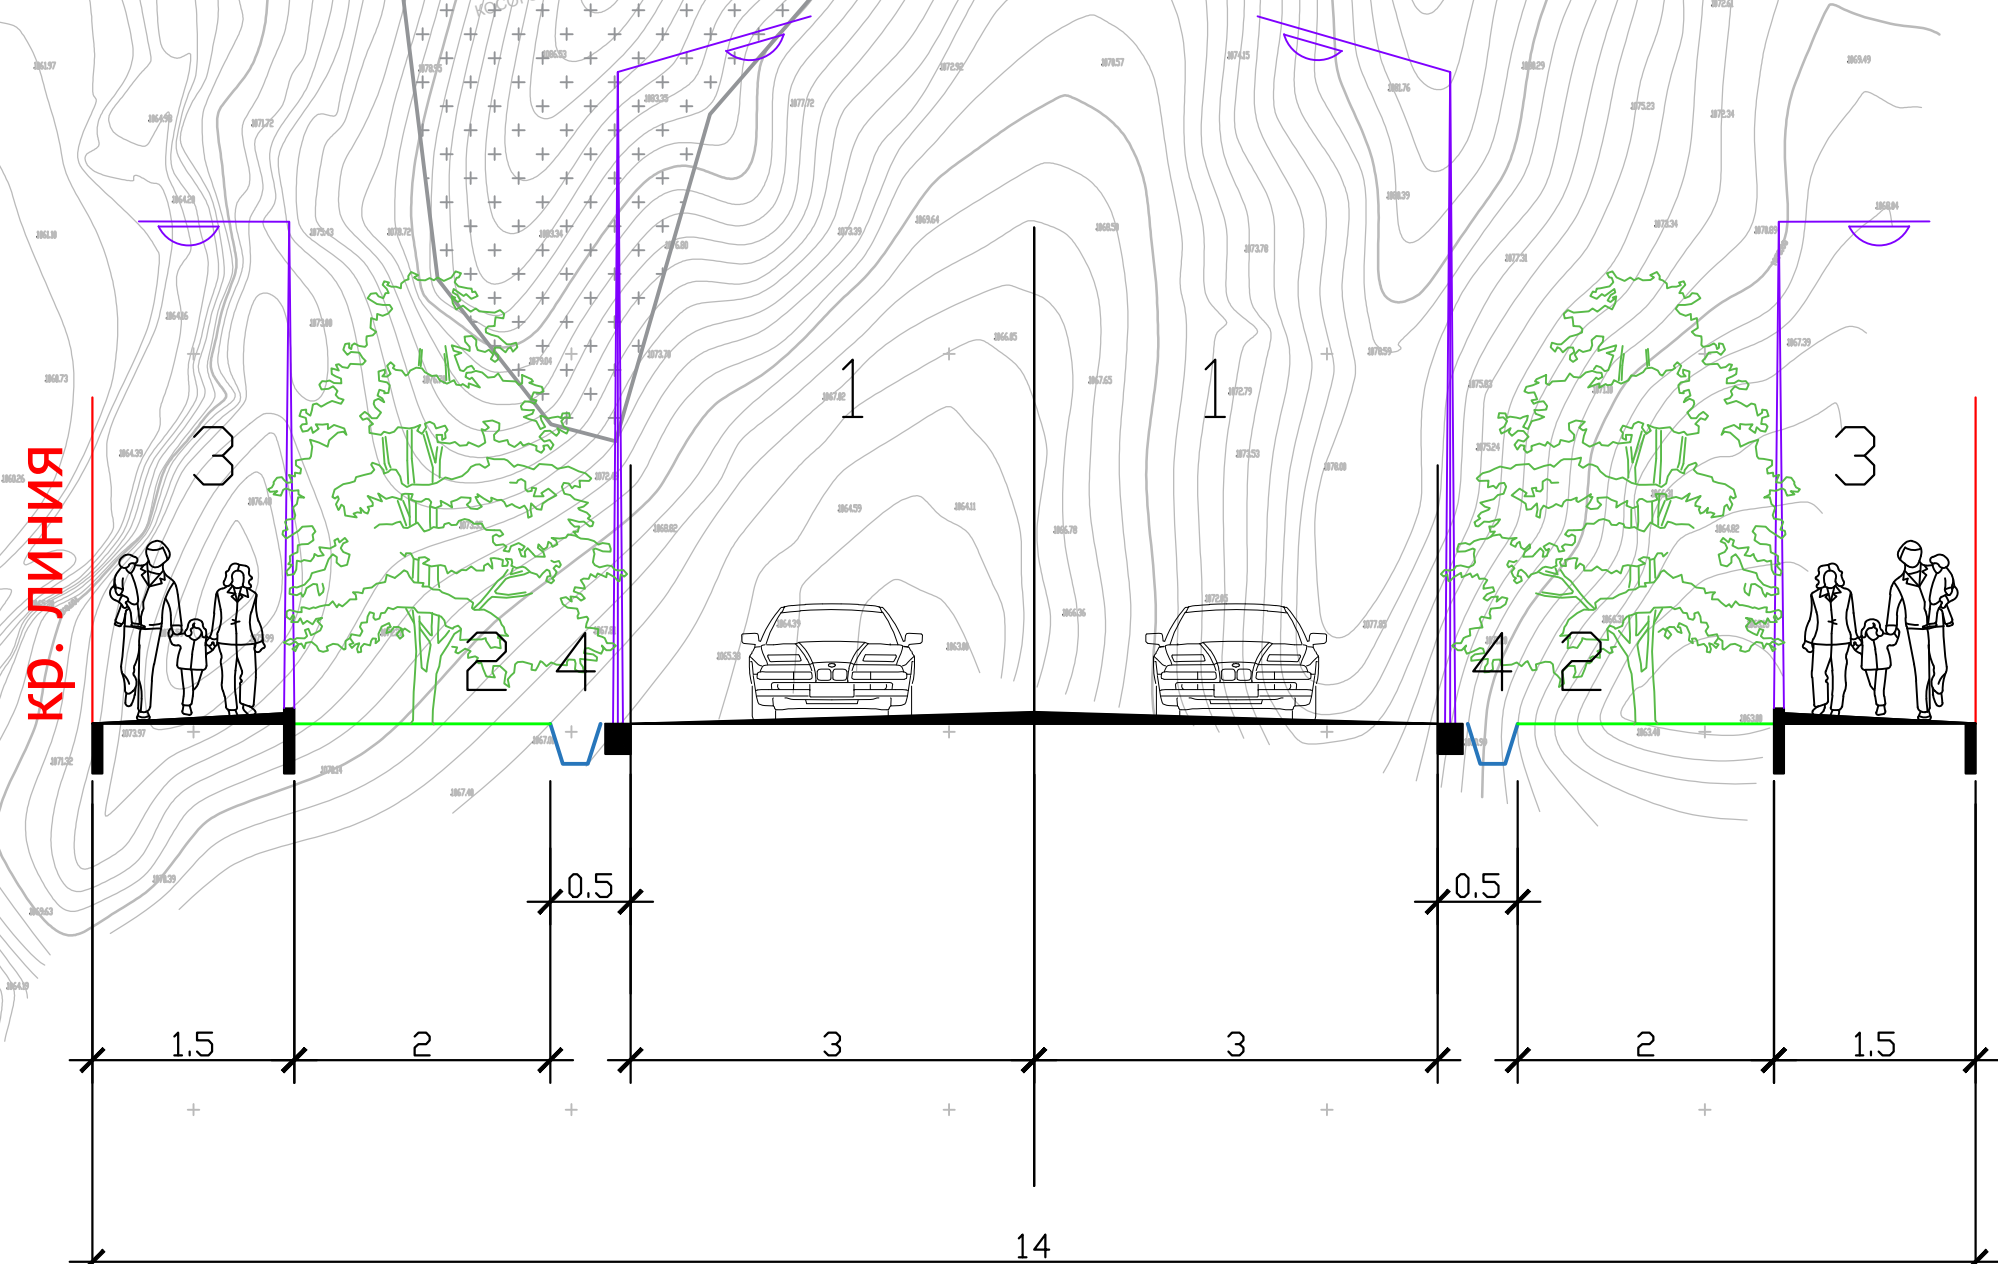

1 - 1
Улицы общепоселкового значения
регулируемого движения
(2 полосы движения транспорта)

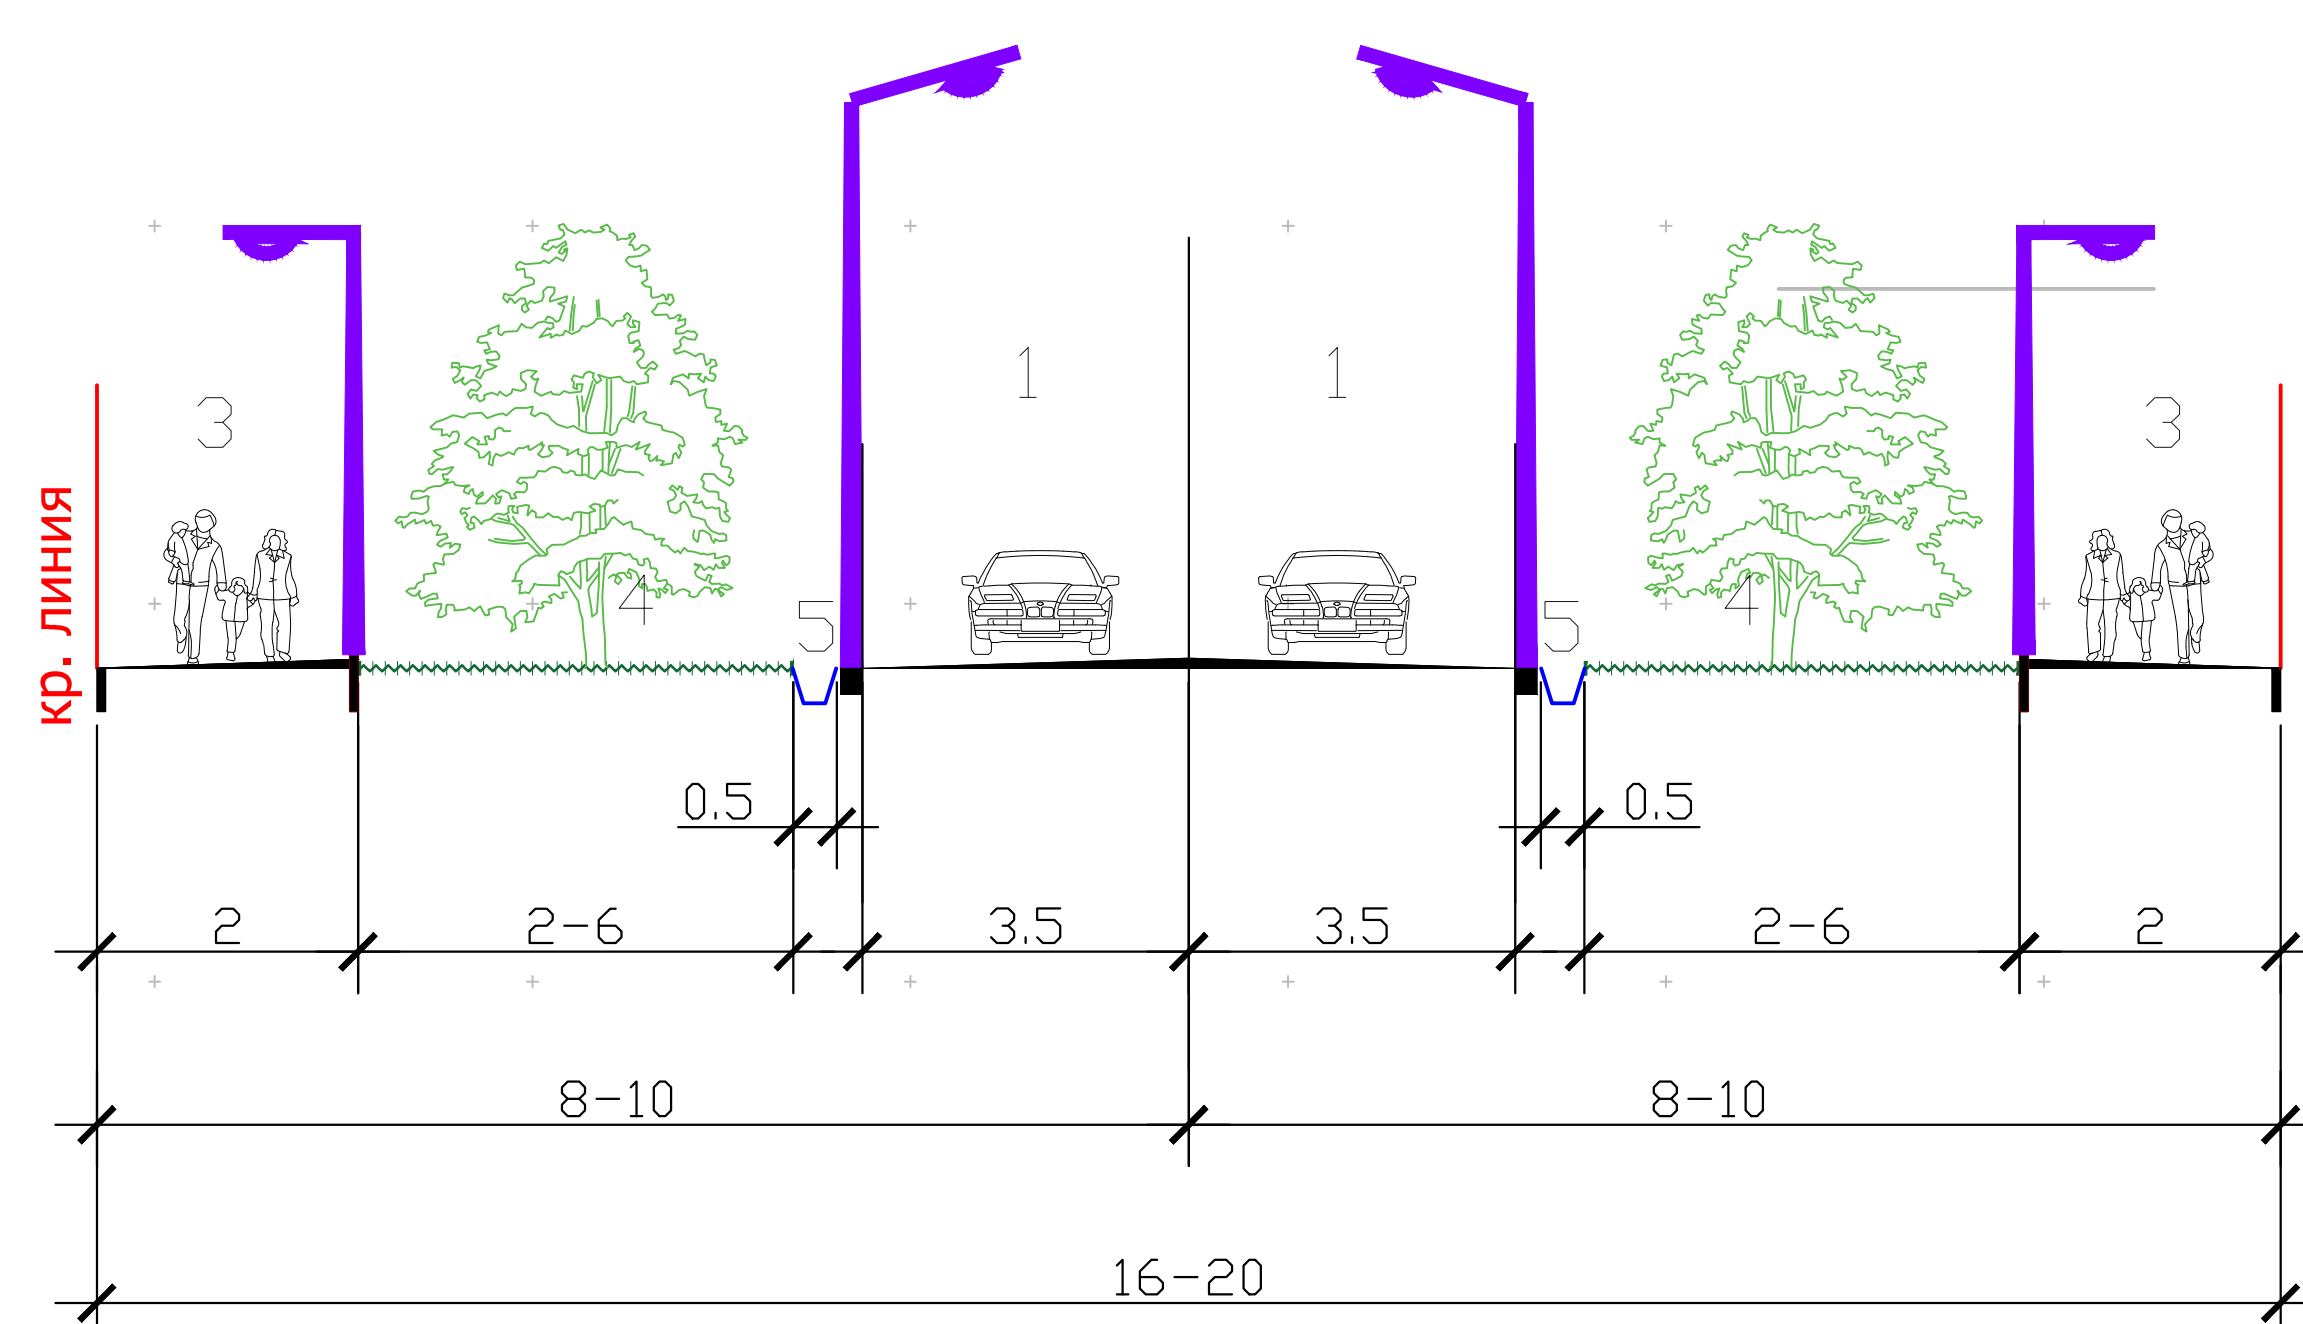

0 - 0
Улицы общепоселкового значения
регулируемого движения
(4 полосы движения транспорта)

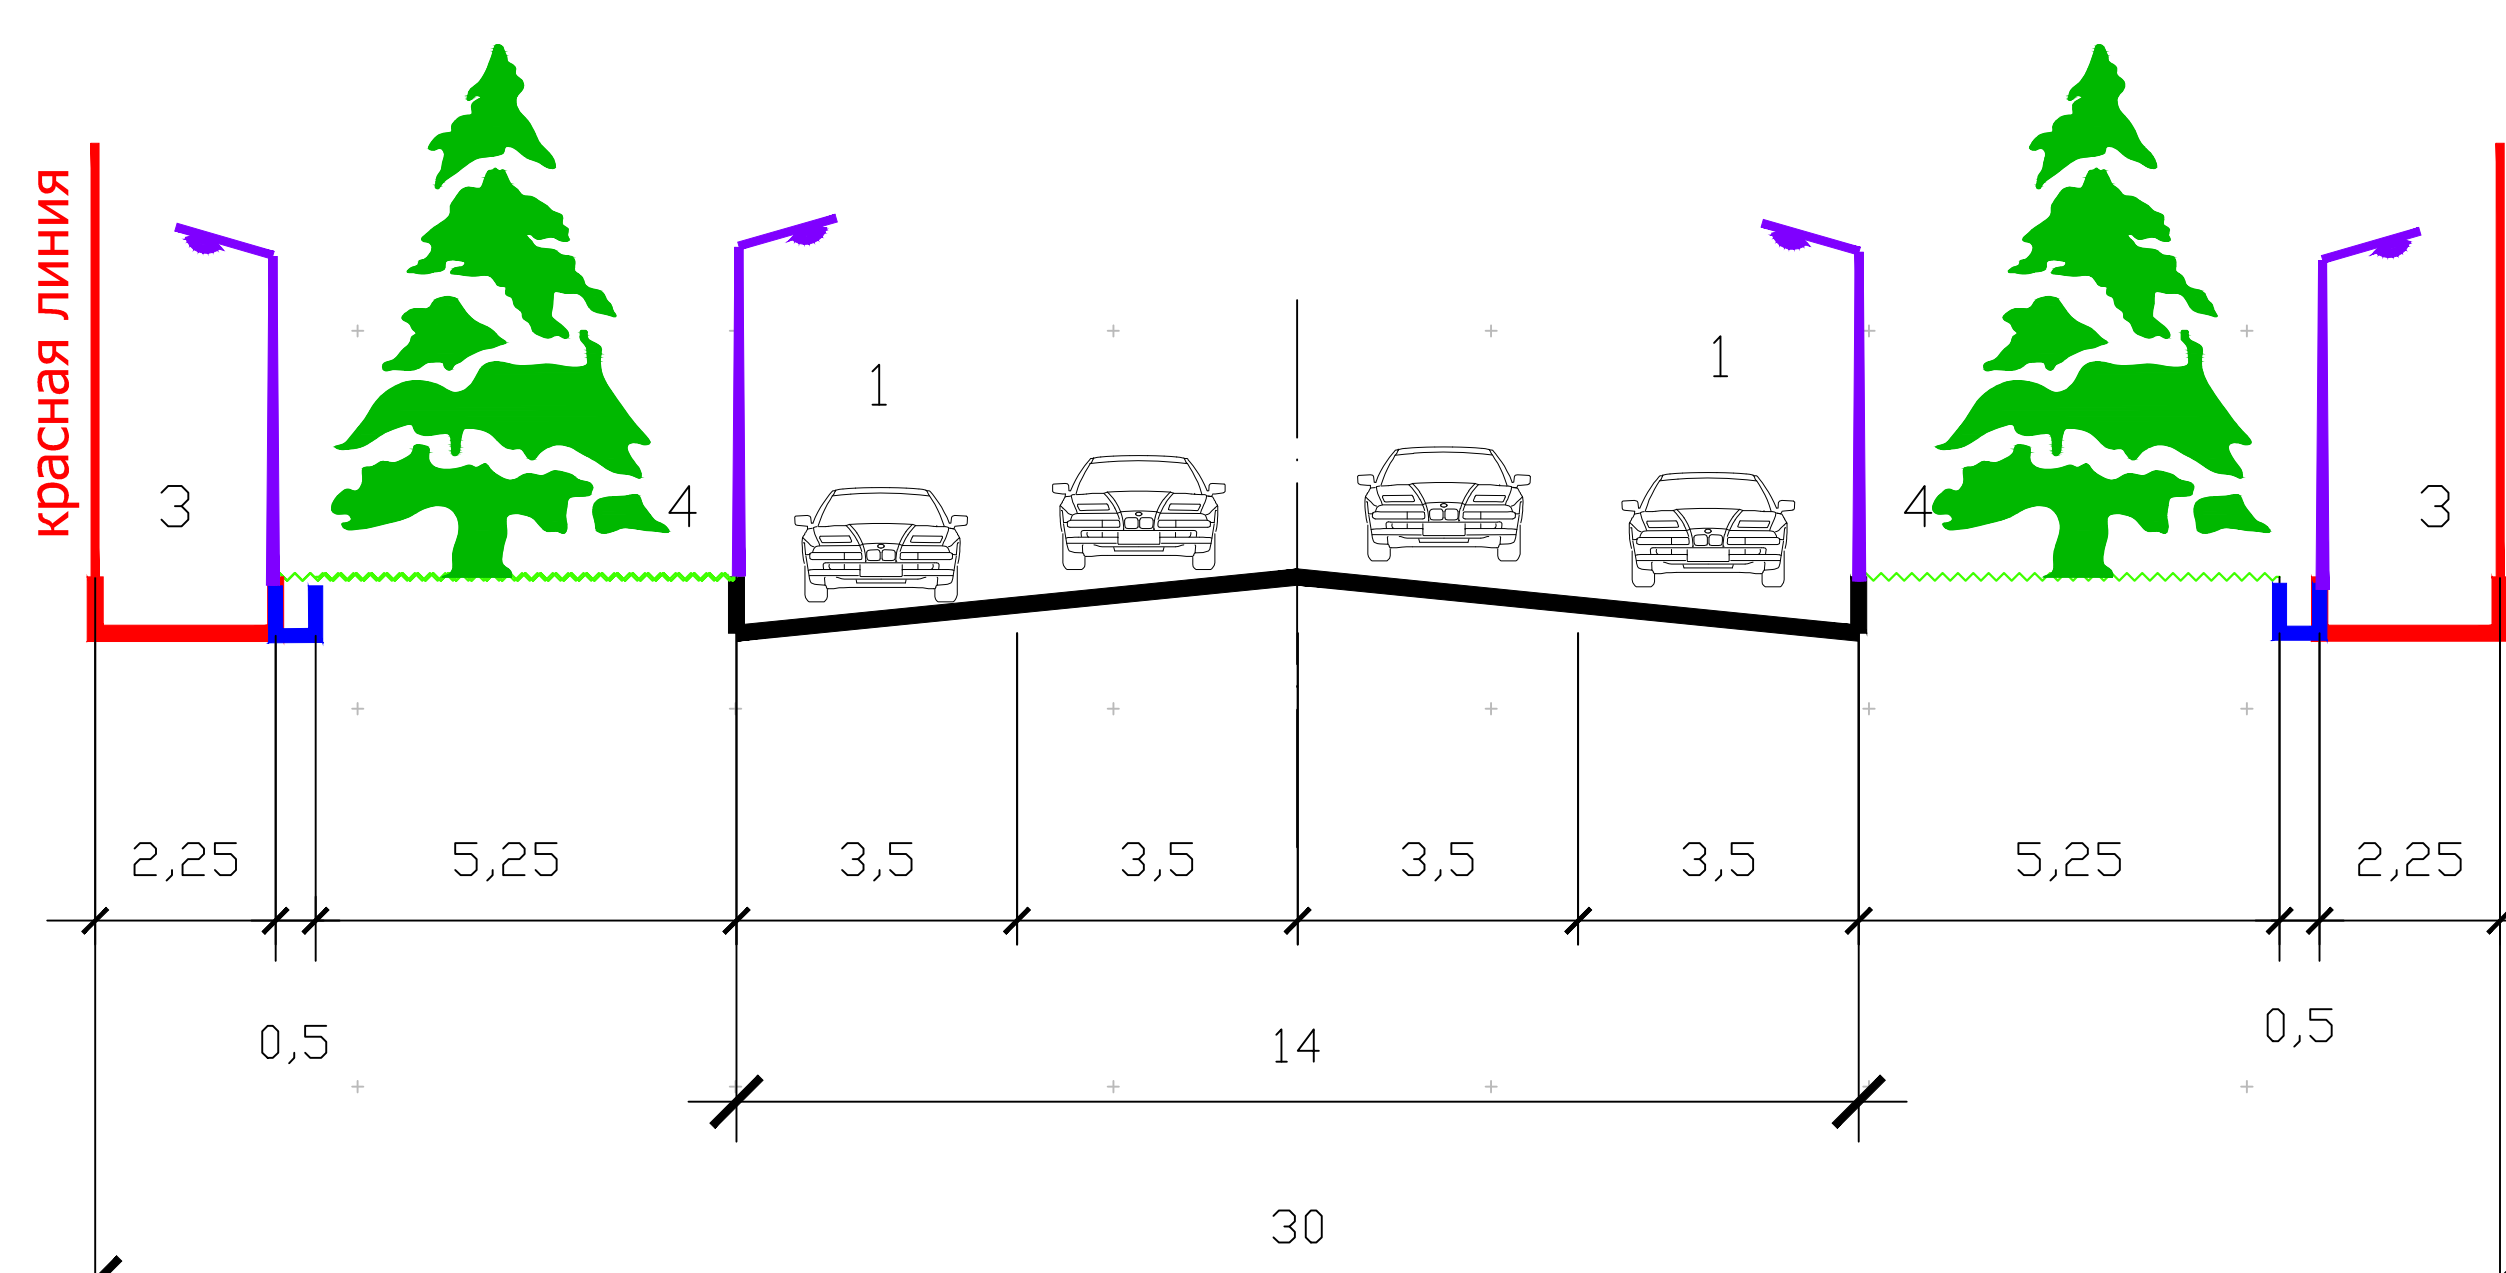

(размеры всех элементов даны в метрах);

договорности	фамилия	подпись	№718-04/2024 от 09.09.2024г.		
зам.инст.	Орловских А.О.		Генеральный план с.Улук Адылского района Жапан-Абдской области заказчик: Кос-Добэ эялэс оюмүтү Схема улично-транспортной сети и внешнего транспорта		
ГАП	Тогобаев К.				
инж.пр.	Асанкулова Ж.Ж.				
инж.пр.	Асанкулова Ж.Ж.				
инж.пр.	Алдарбеков Кыды А.				
инж.пр.	Тогобаев уулу К.		этадия	лист	масштаб
инж.пр.	Осмоиловна М.		П1		М 1:2000
пр.			ГПМ градостроительства и архитектуры		