
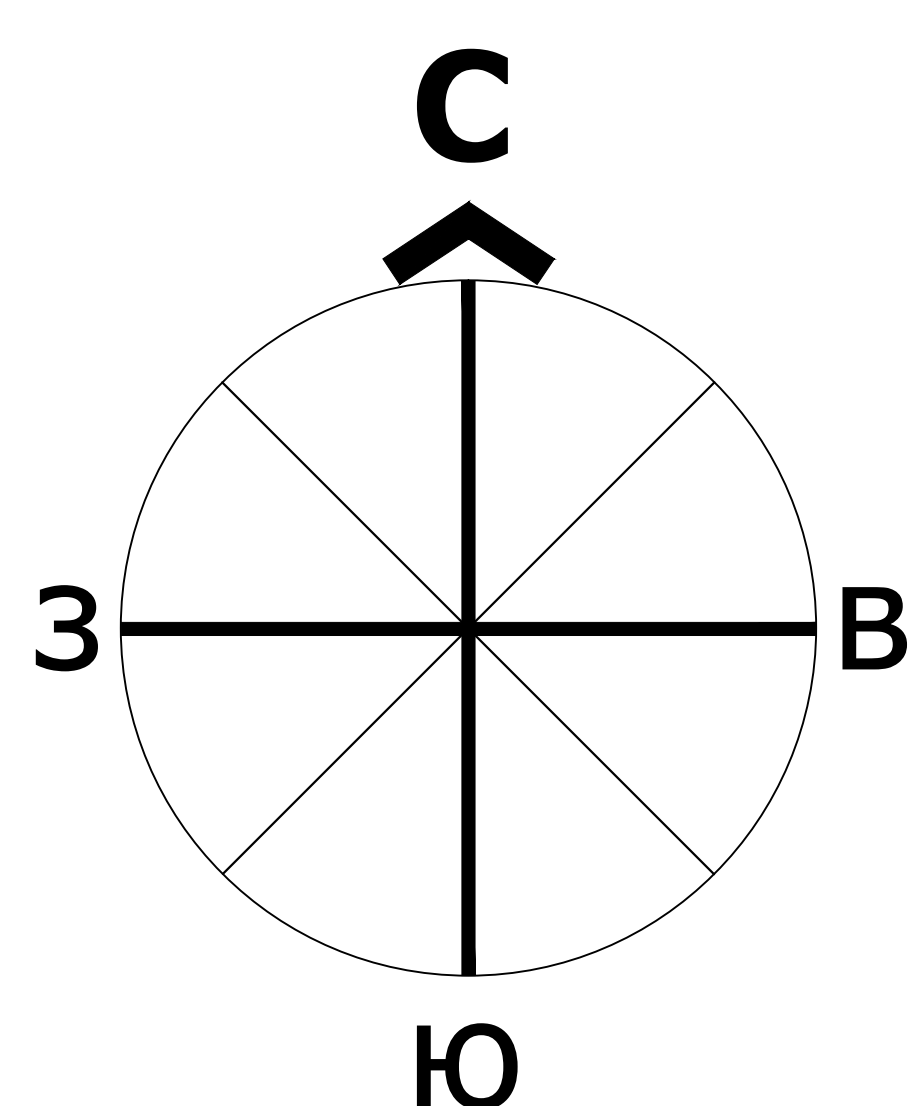
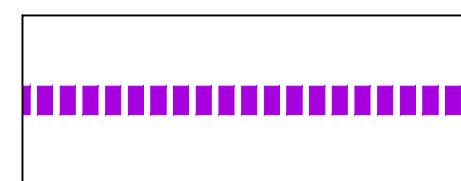
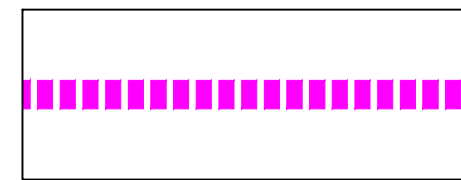
 


M1:2000

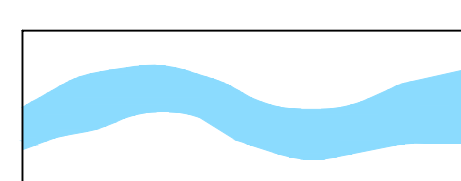


УСЛОВНЫЕ ОБОЗНАЧЕНИЯ


- | | |
|--|-------------------------------------|
|  | Фактическая (сложившаяся) граница |
|  | Проектируемая граница |
|  | Проектируемые красные линии |
|  | Реки, магистральные каналы, водоемы |
|  | Главные поселковые улицы |
|  | Улицы и дороги местного значения |
|  | Проезды |
|  | Мосты и переправы |

ЭКСПЛИКАЦИЯ:


1. Школа им. Ж.Султанова №8 на 225 учащихся мест
2. Детский сад С.Касымбекова на 50 учащихся мест
3. Стадион
4. Проектируемый ФАП
5. Проектируемый детский сад
6. Проектируемая спортивная школа

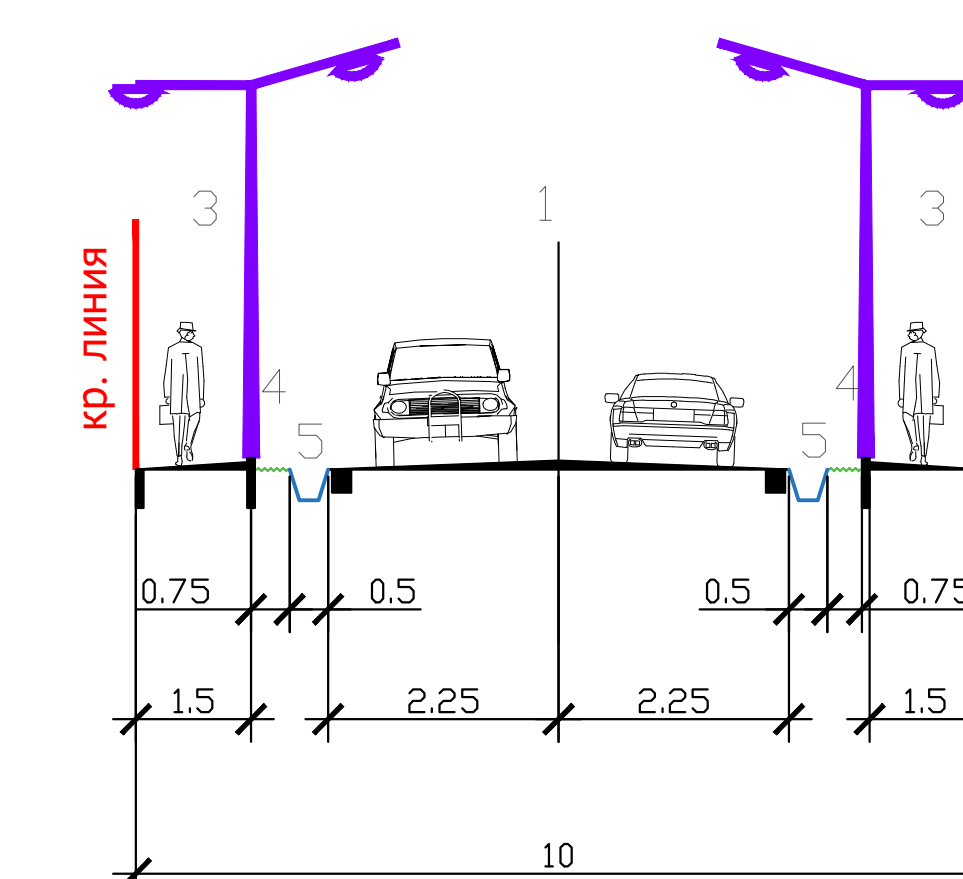


3 - 3
Улицы местного значения
(2 полосы движения транспорта)

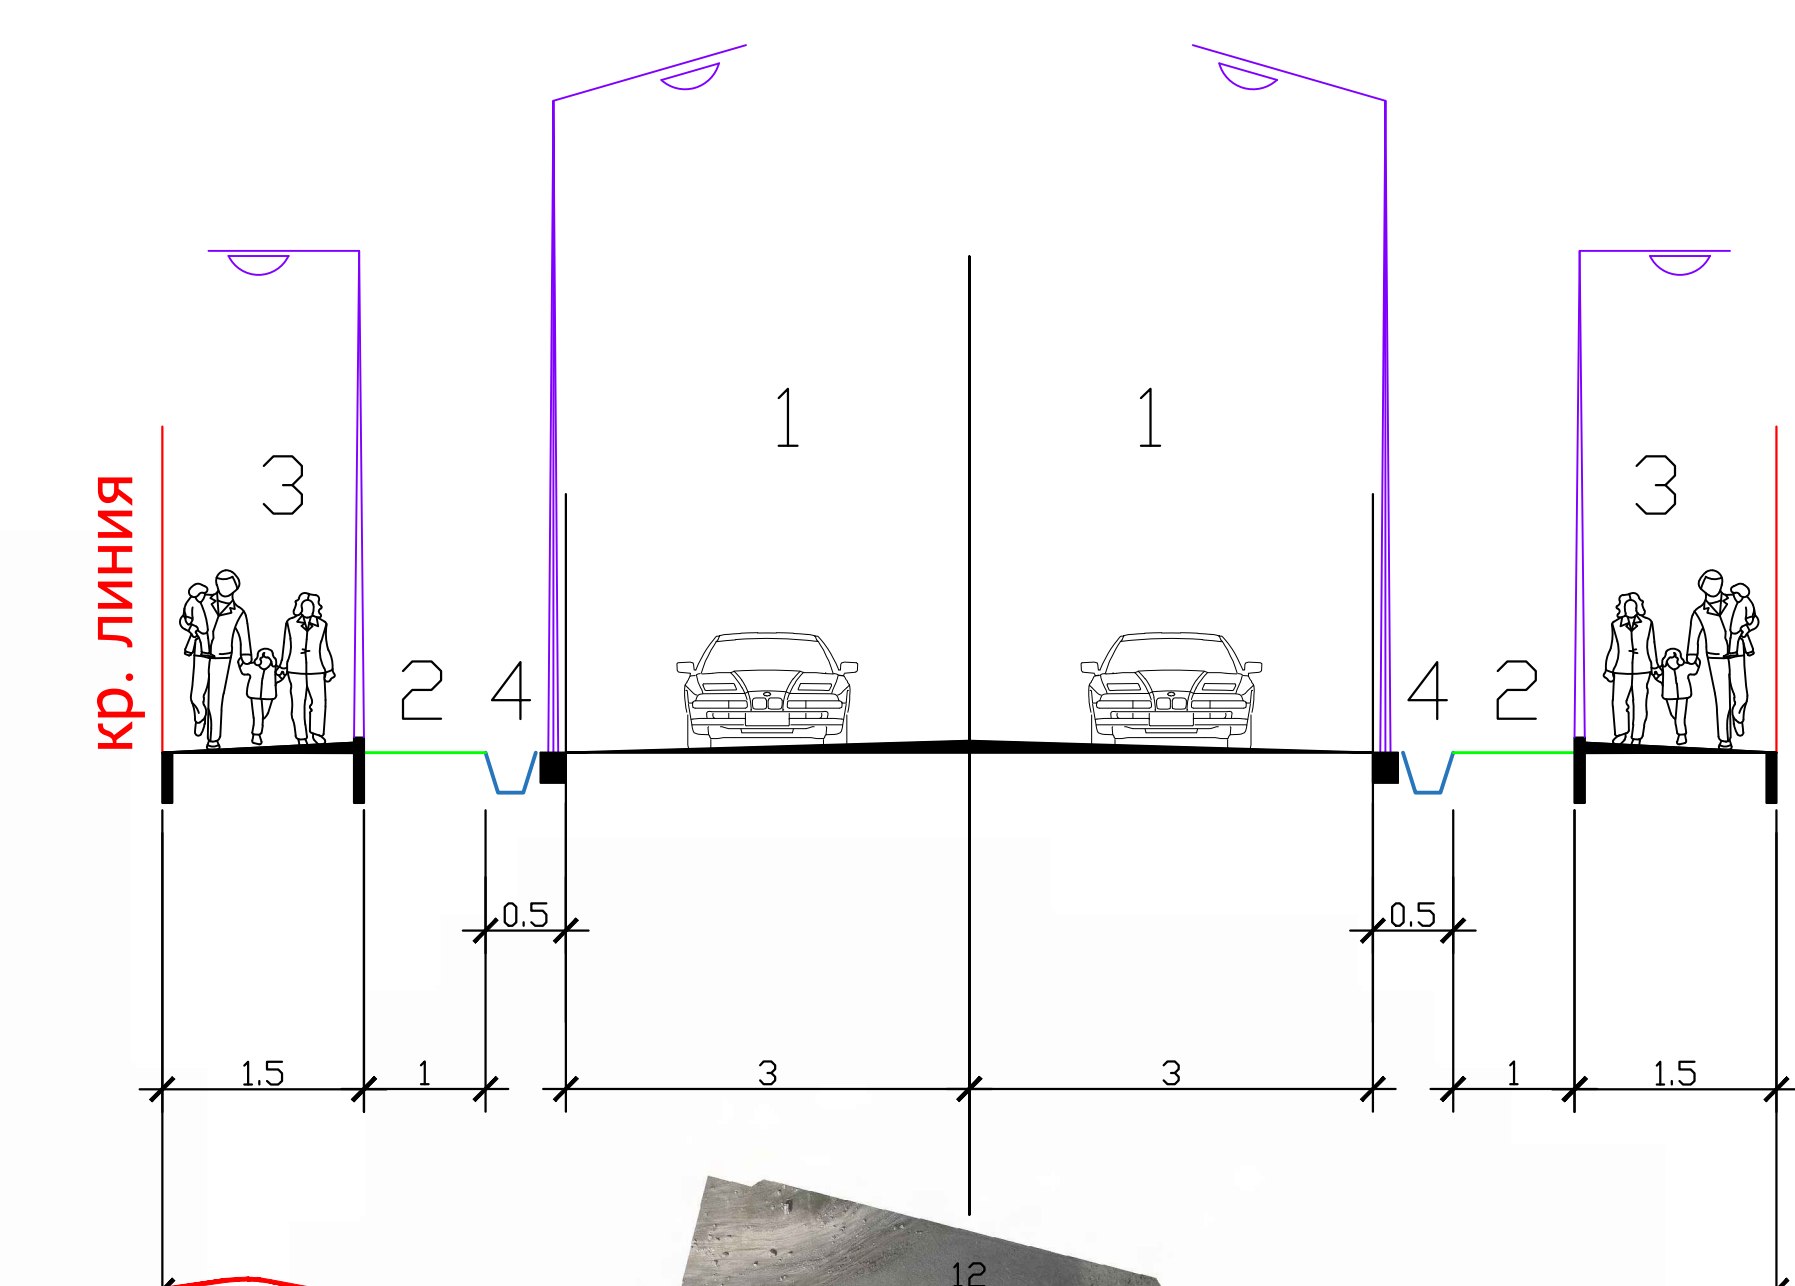


2 - 2
Улицы местного значения
(2 полосы движения транспорта)

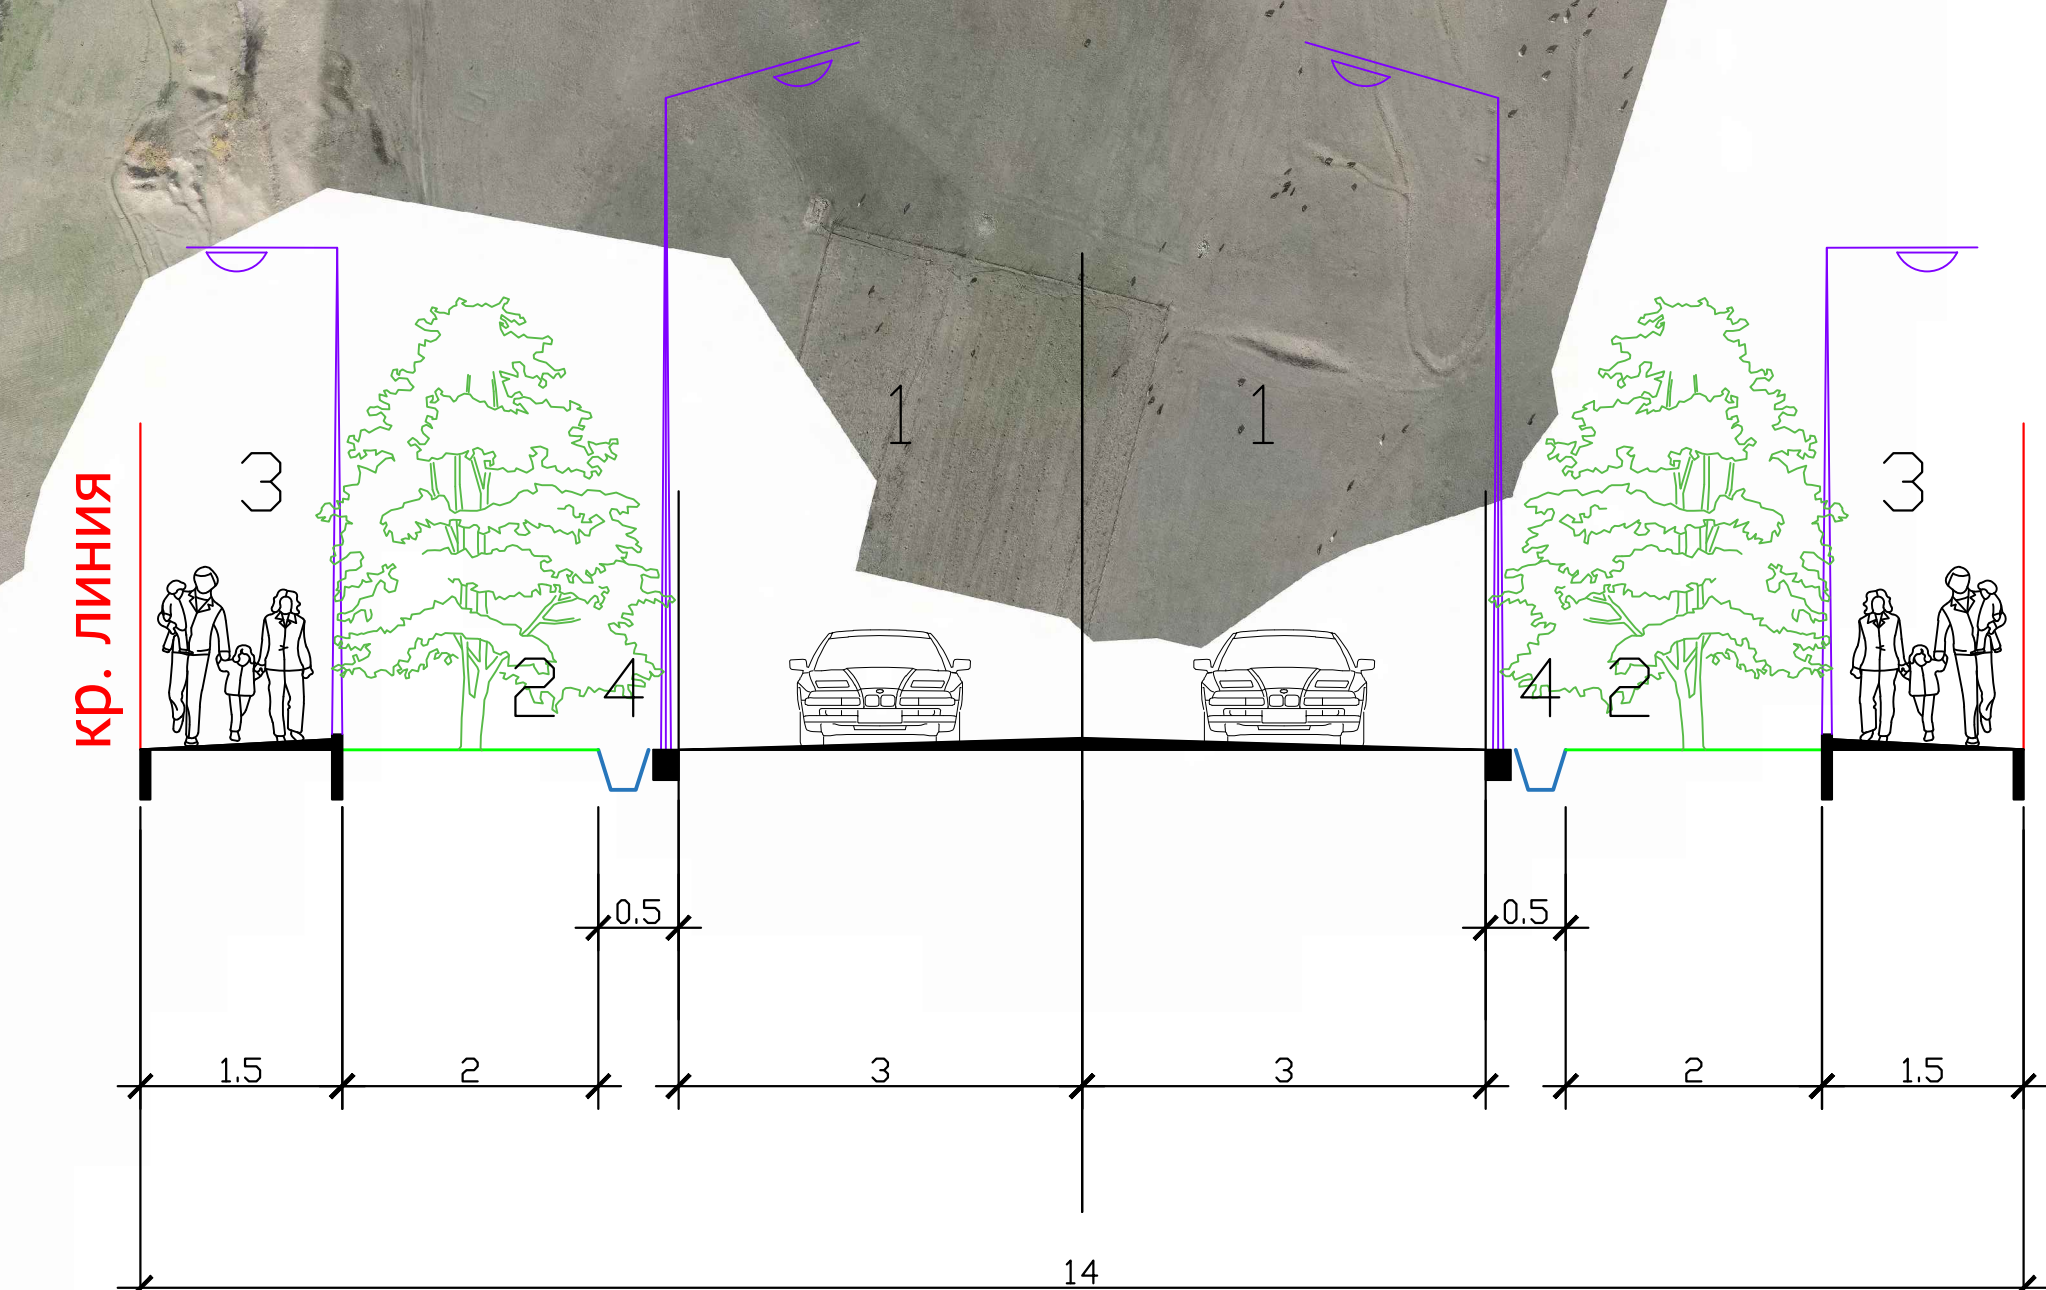

1 - 1
Улицы общепоселкового значения
регулируемого движения
(2 полосы движения транспорта)

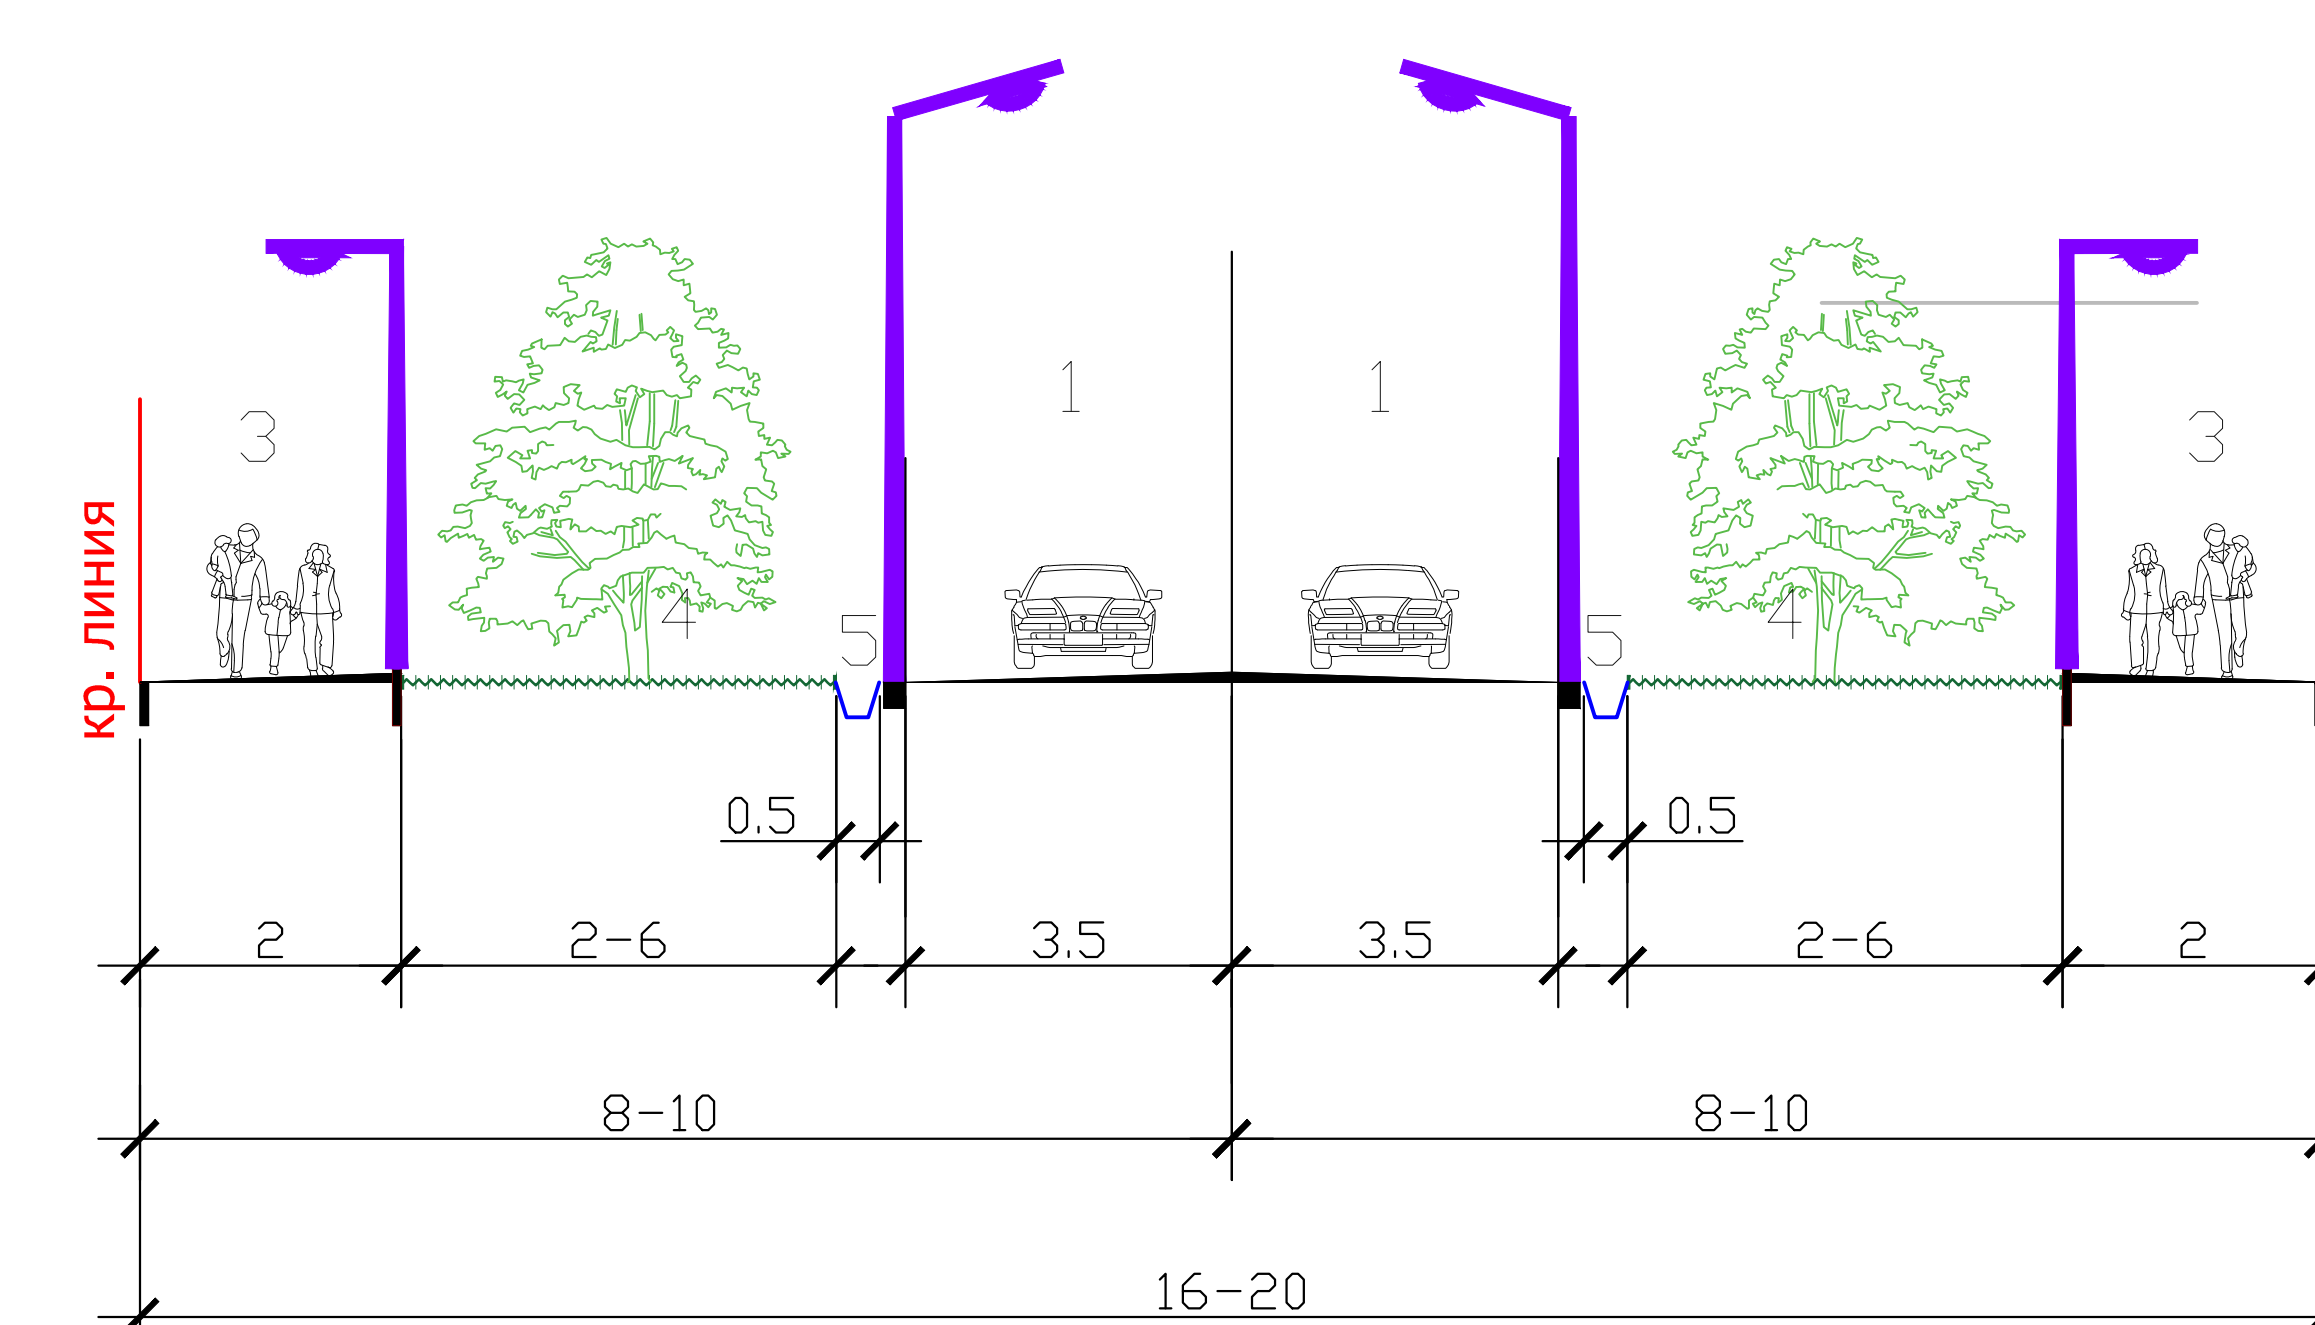

0 - 0
Улицы общепоселкового значения
регулируемого движения
(4 полосы движения транспорта)

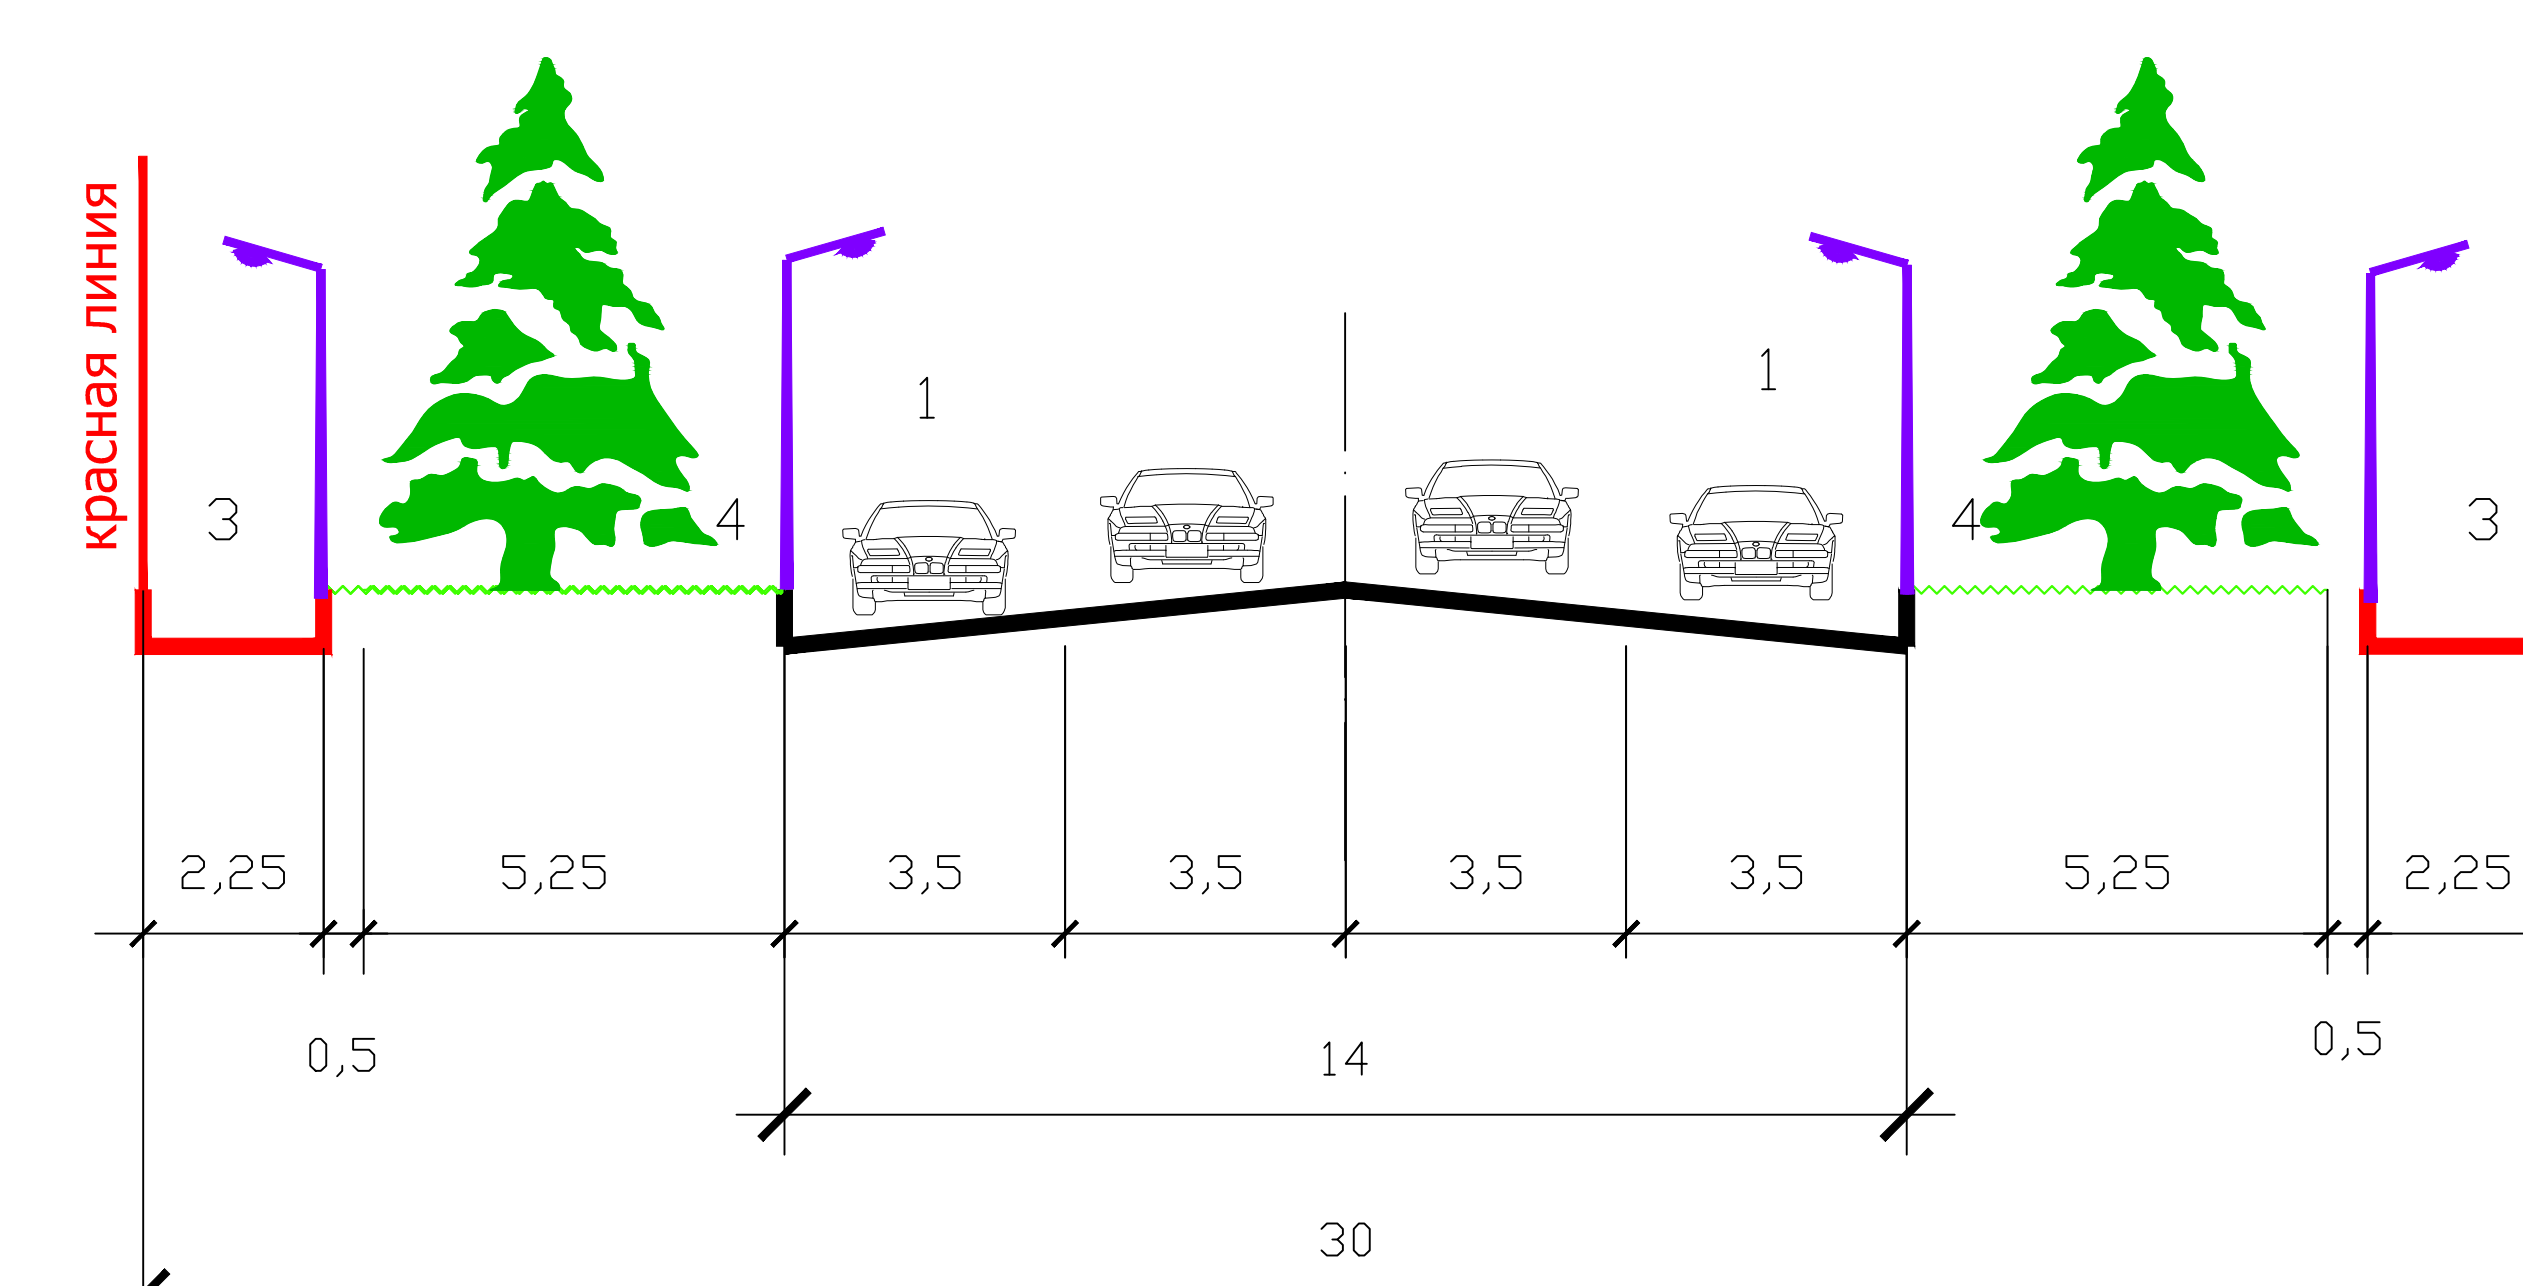

(размеры всех элементов даны в метрах);

достоинство	фамилия	подпись	№17/04/2024 от 09.08.2024г.		
зам. инст.	Орлбеков А.О.		Генеральный пт. - Улус Ахыйоого района Жапан-Абайской области		
ГАП	Толубаев К.				
вед. зр.	Асанкулова А. Ж.				
вед. зр.	Асановокова Ж.М.				
вед. зр.	Абдыраман уулы А.				
вед. зр.	Токтобеков уулы К.	заклуж.: Коса-Добо аял оомуту	отдание	лист	максимум
зр.	Осмоноватова М.		ПТ		М 1.00
Смена взрослых			ГПИ градоостроительств		